




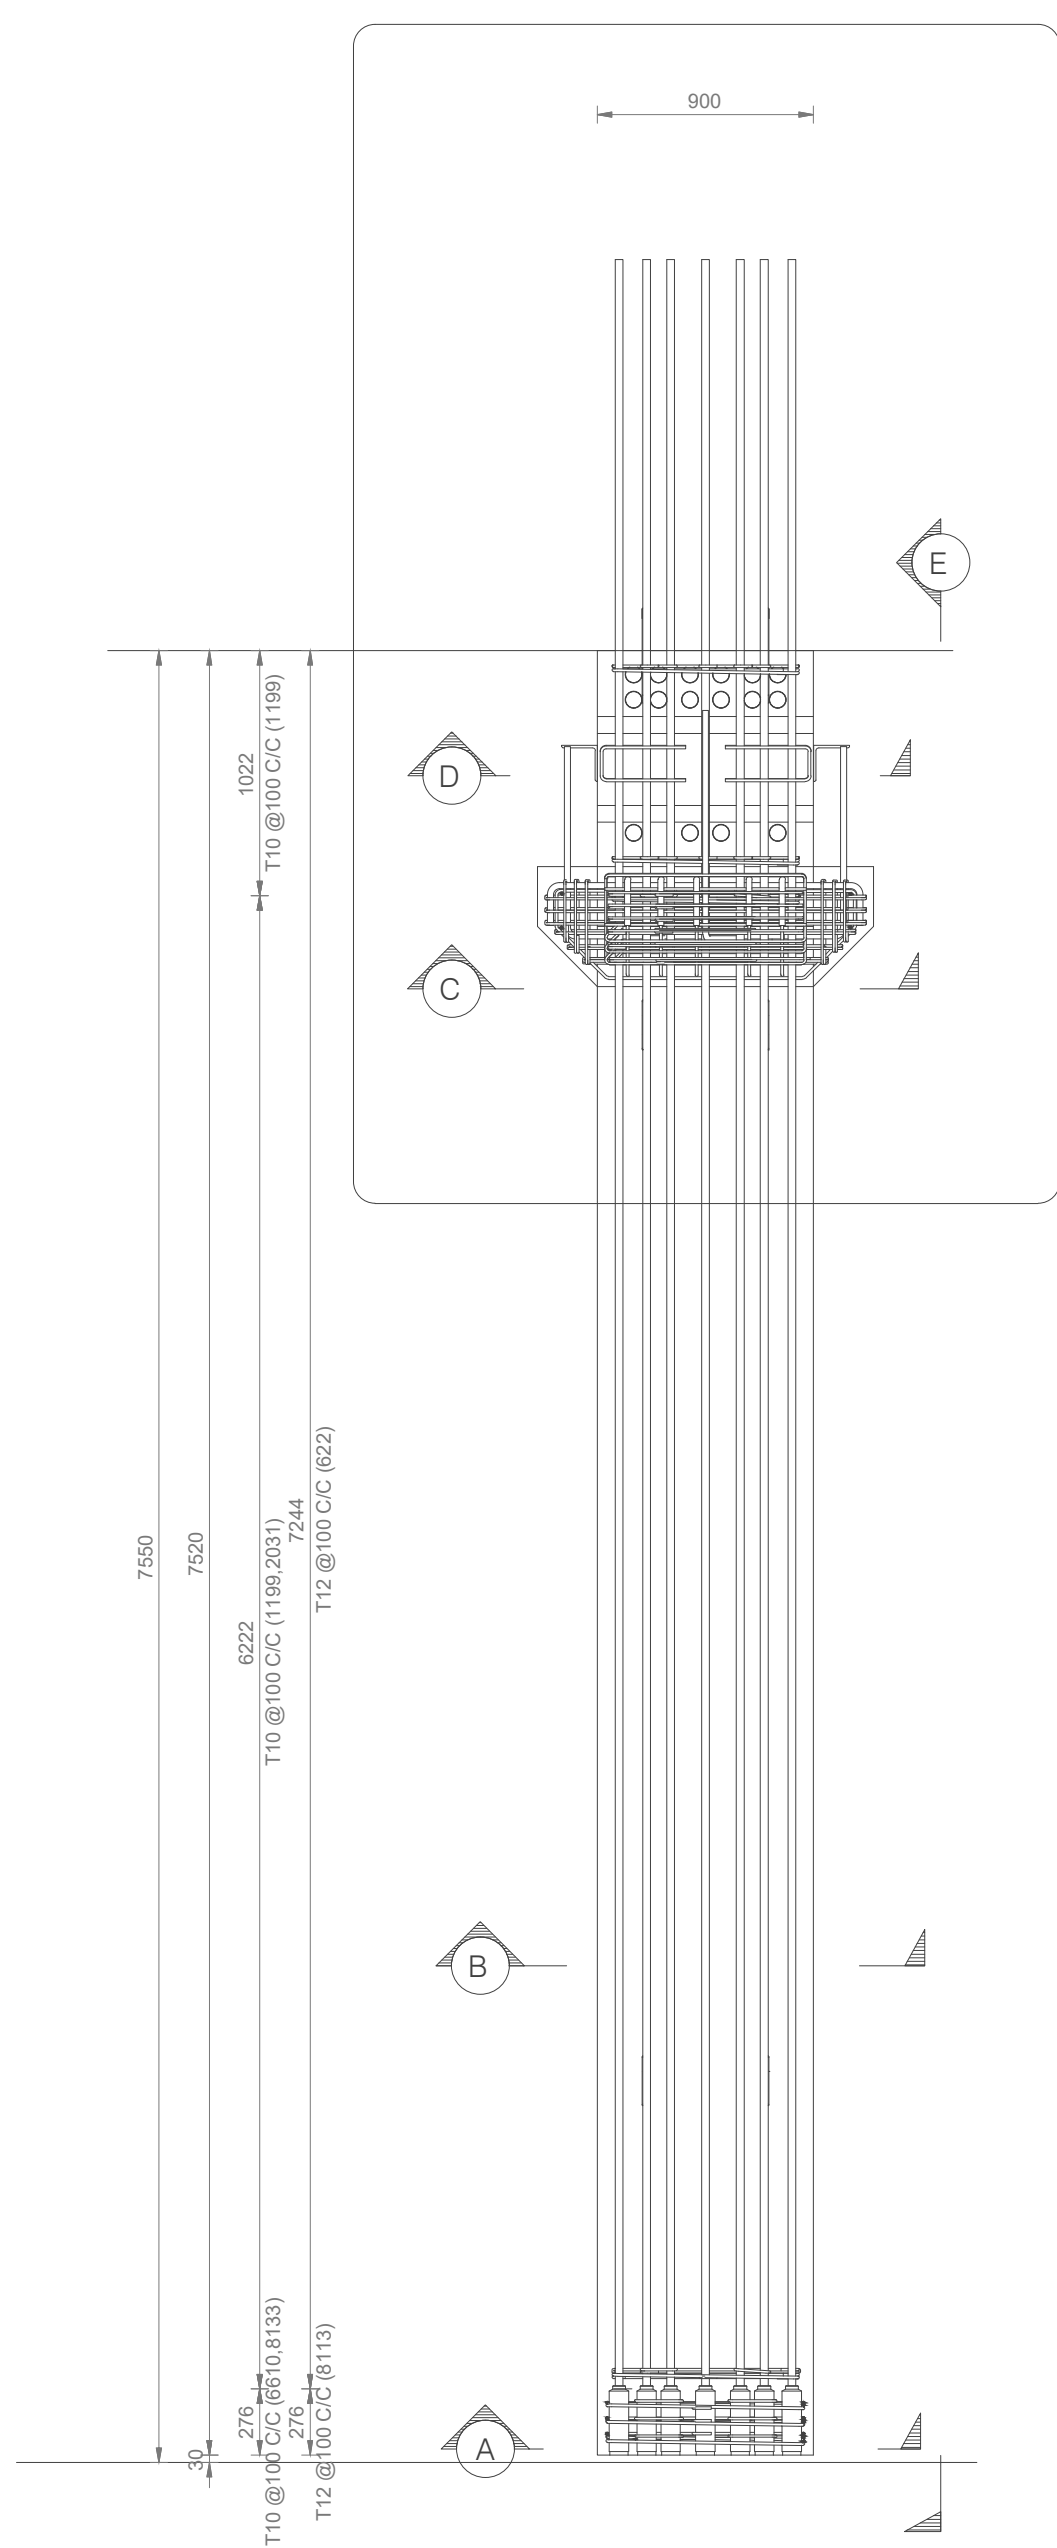

REINFORCEMENT DETAILS OF PRECAST COLUMN
SCALE = 1 : 30

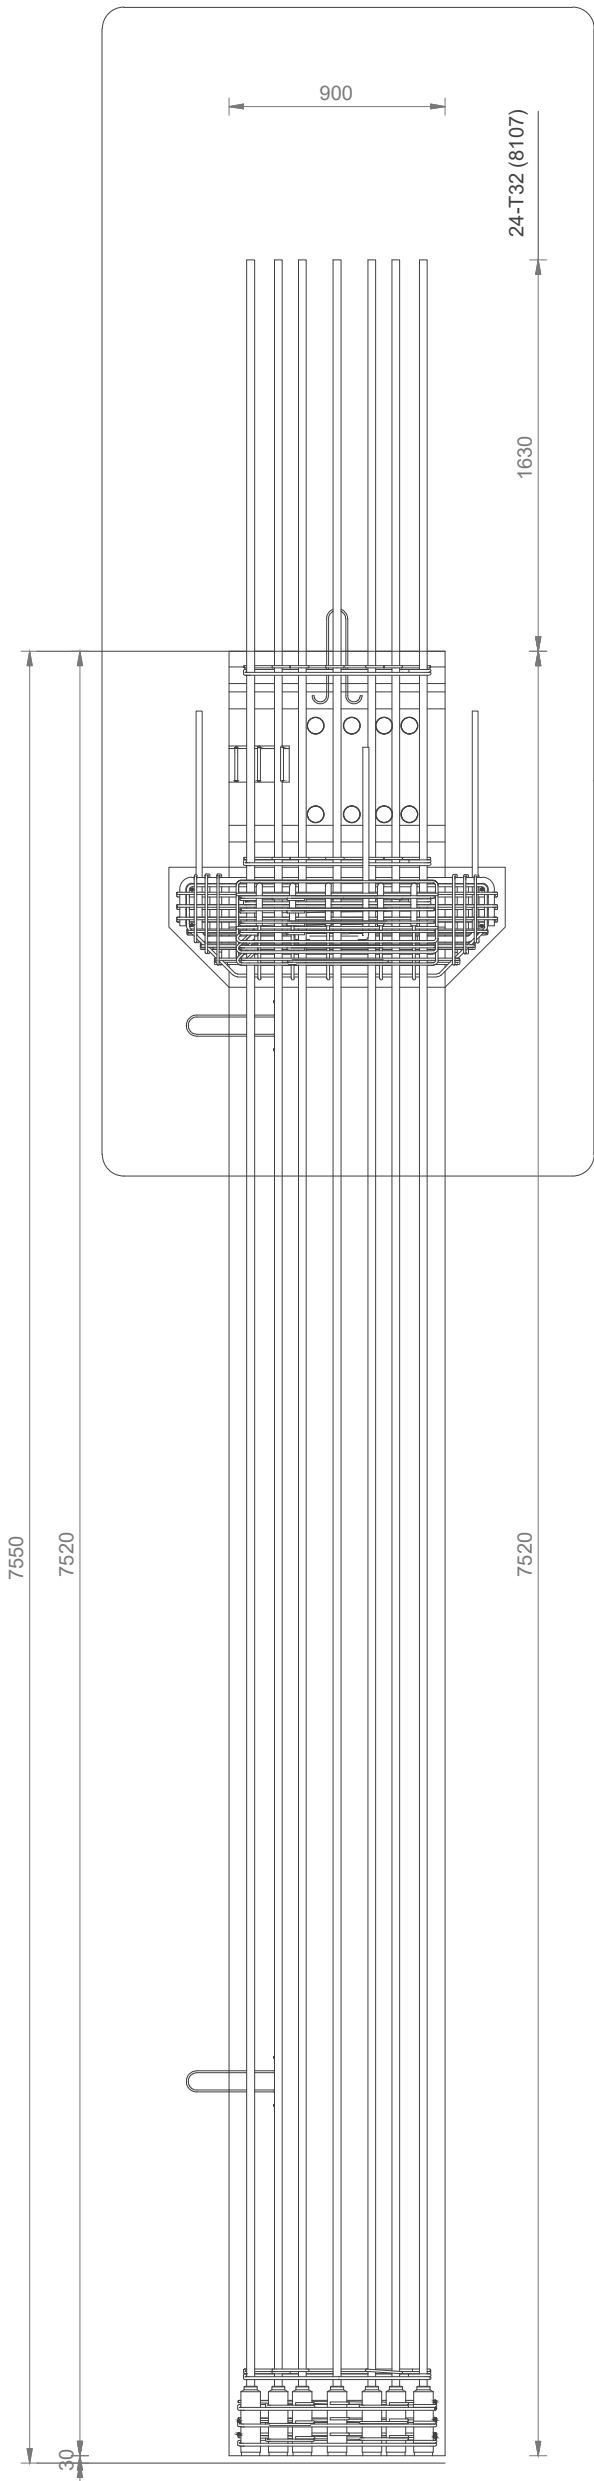


ELEVATION
SCALE - 1 : 30

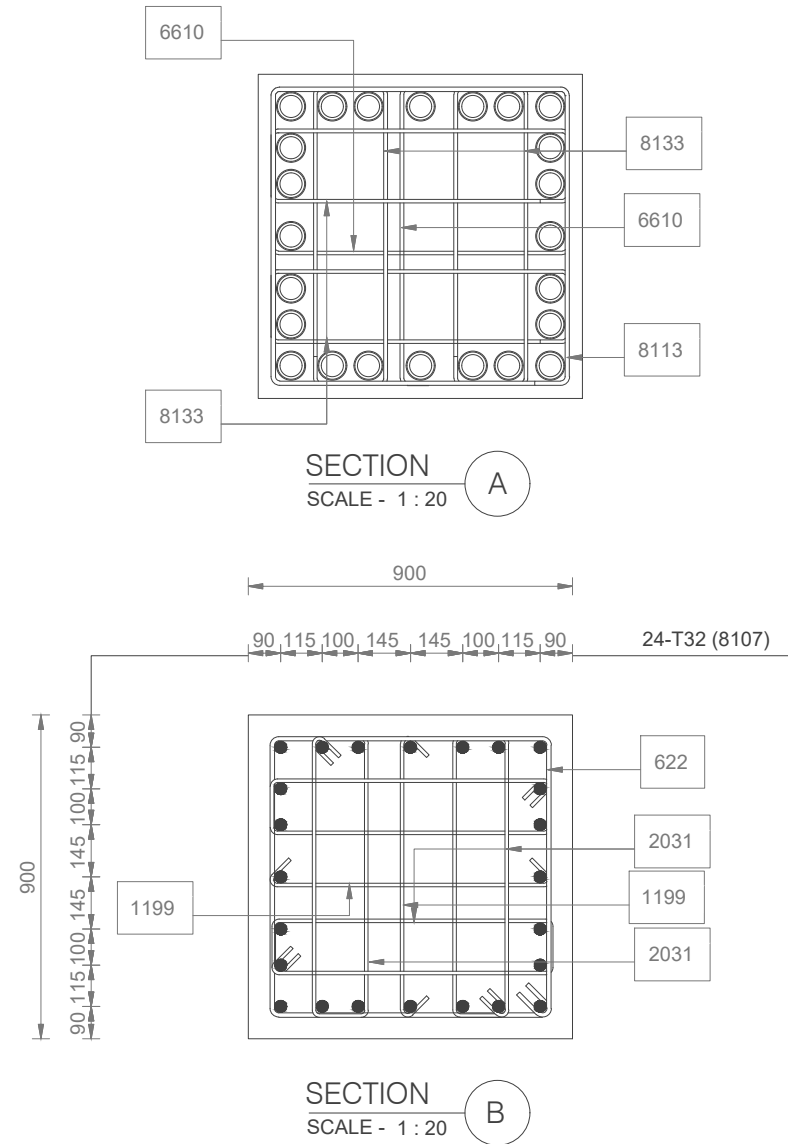


SECTION A
SCALE - 1 : 20


SECTION B
SCALE - 1 : 20

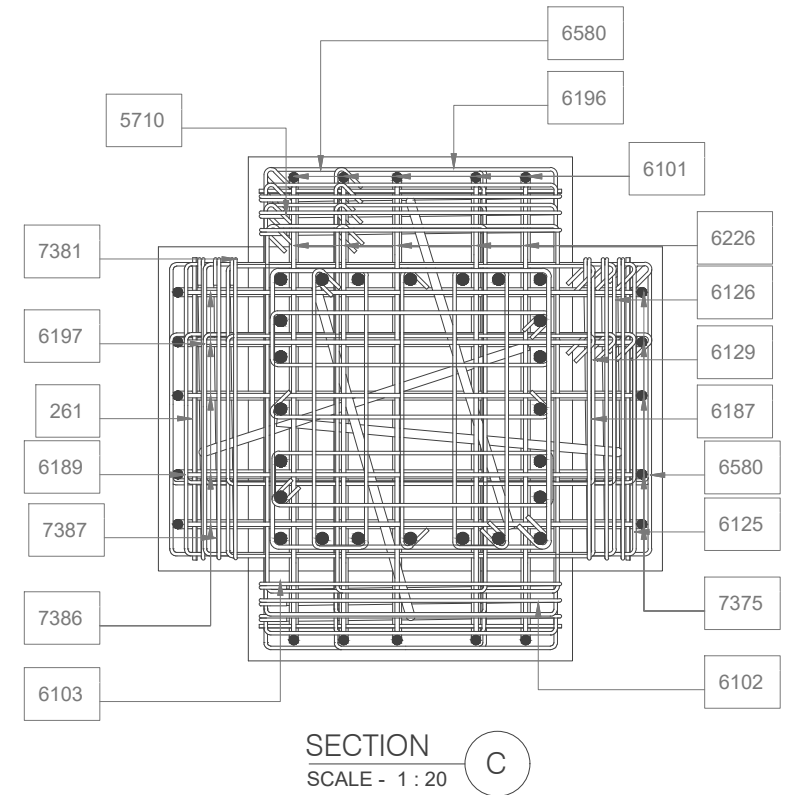

SECTION C
SCALE - 1 : 20

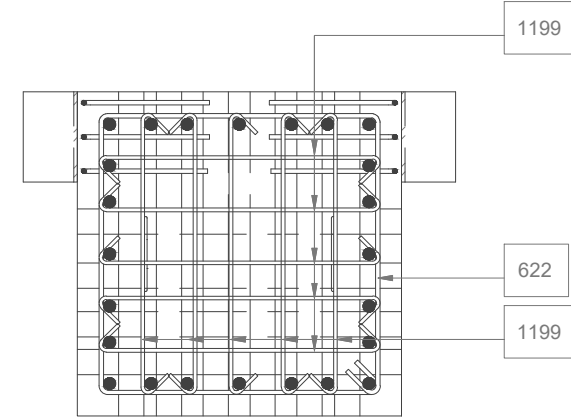


SECTION D
SCALE - 1 : 20

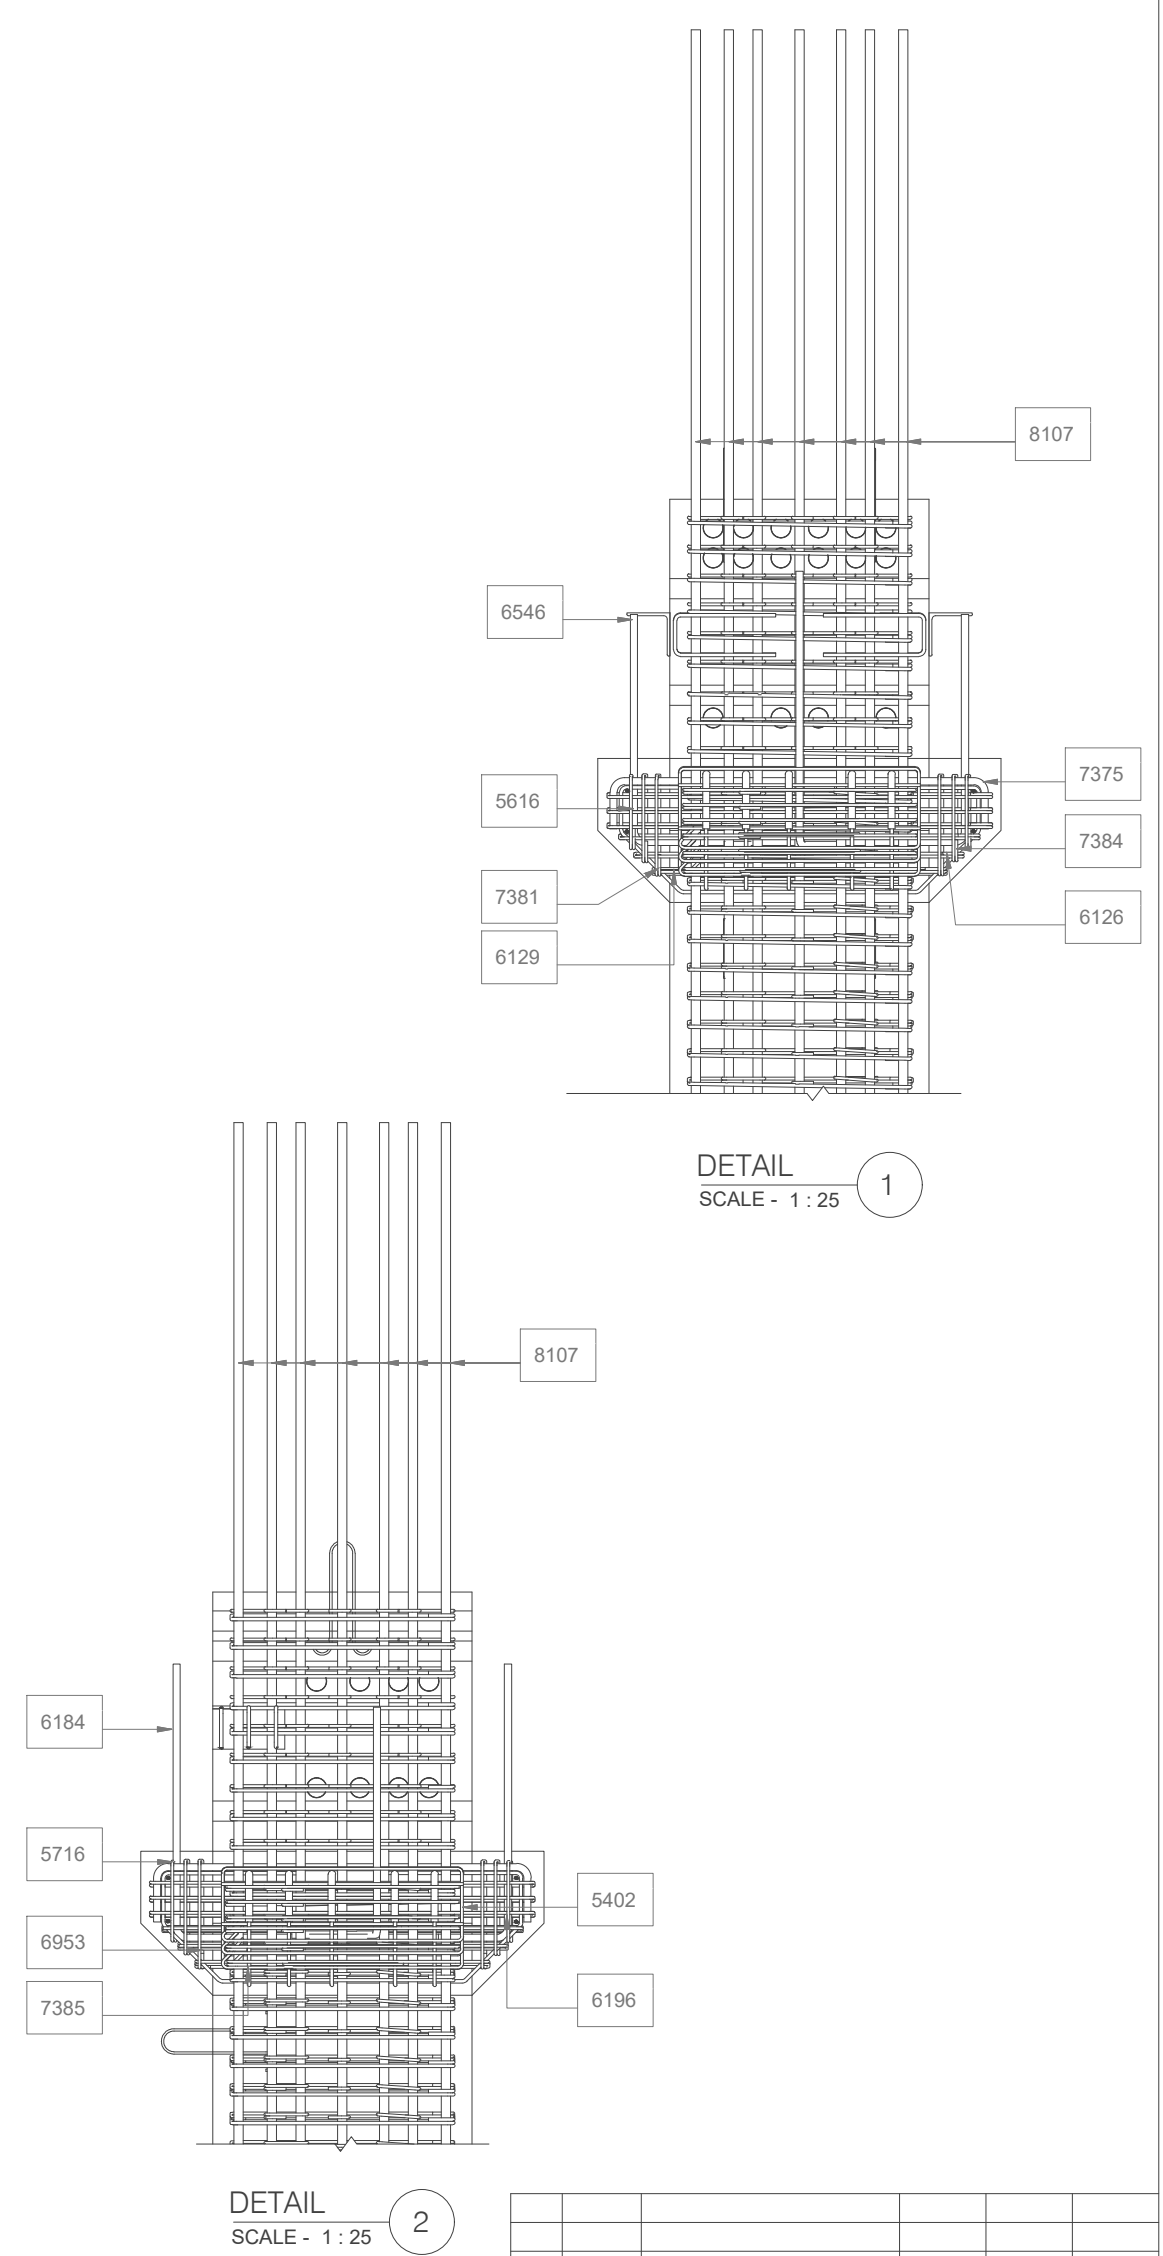


DETAIL 1
SCALE - 1 : 25

DETAIL 2
SCALE - 1 : 25




R0	02-07-2026	GOOD FOR CONSTRUCTION	SPS	SAM	SDK
REV.	DATE	DRAWING STATUS	DRAWN BY	CHECKED BY	APPROVED BY
REVISION HISTORY					
STRUCTURAL CONSULTANT :		PPS ENGINEERING CONSULTANTS LLP.			
		FIRST FLOOR, SERVICE BUILDING, BAFI BHAVAN, DR. MANIBHAI DESAI NAGAR, WARJE, PUNE 411058, INDIA. EMAIL : design@ppsel.in WEB SITE : www.ppspl.in Tel. : + 91 20 25232858			
PROJECT NUMBER		25-4035			
PROJECT NAME		ACXNMI-03			
 <i>Your Growth. Our Priority.</i>		CLIENT			
		ADANICONNEX			
REINFORCEMENT DETAILS OF		N3C-2-C18			
PRECAST COLUMN :					
DWG NUMBER		N3C-2-C18-RF			
RELEASED FOR	APPROVAL	DRAWN	NAME	DATE	SCALE : AS SHOWN
	TENDER	CHECKED	SPS	02-07-2026	
	CONSTRUCTION	✓	SAM	02-07-2026	SIZE : A2
	INFORMATION		APPROVED	SDK	02-07-2026
					REV. : R0

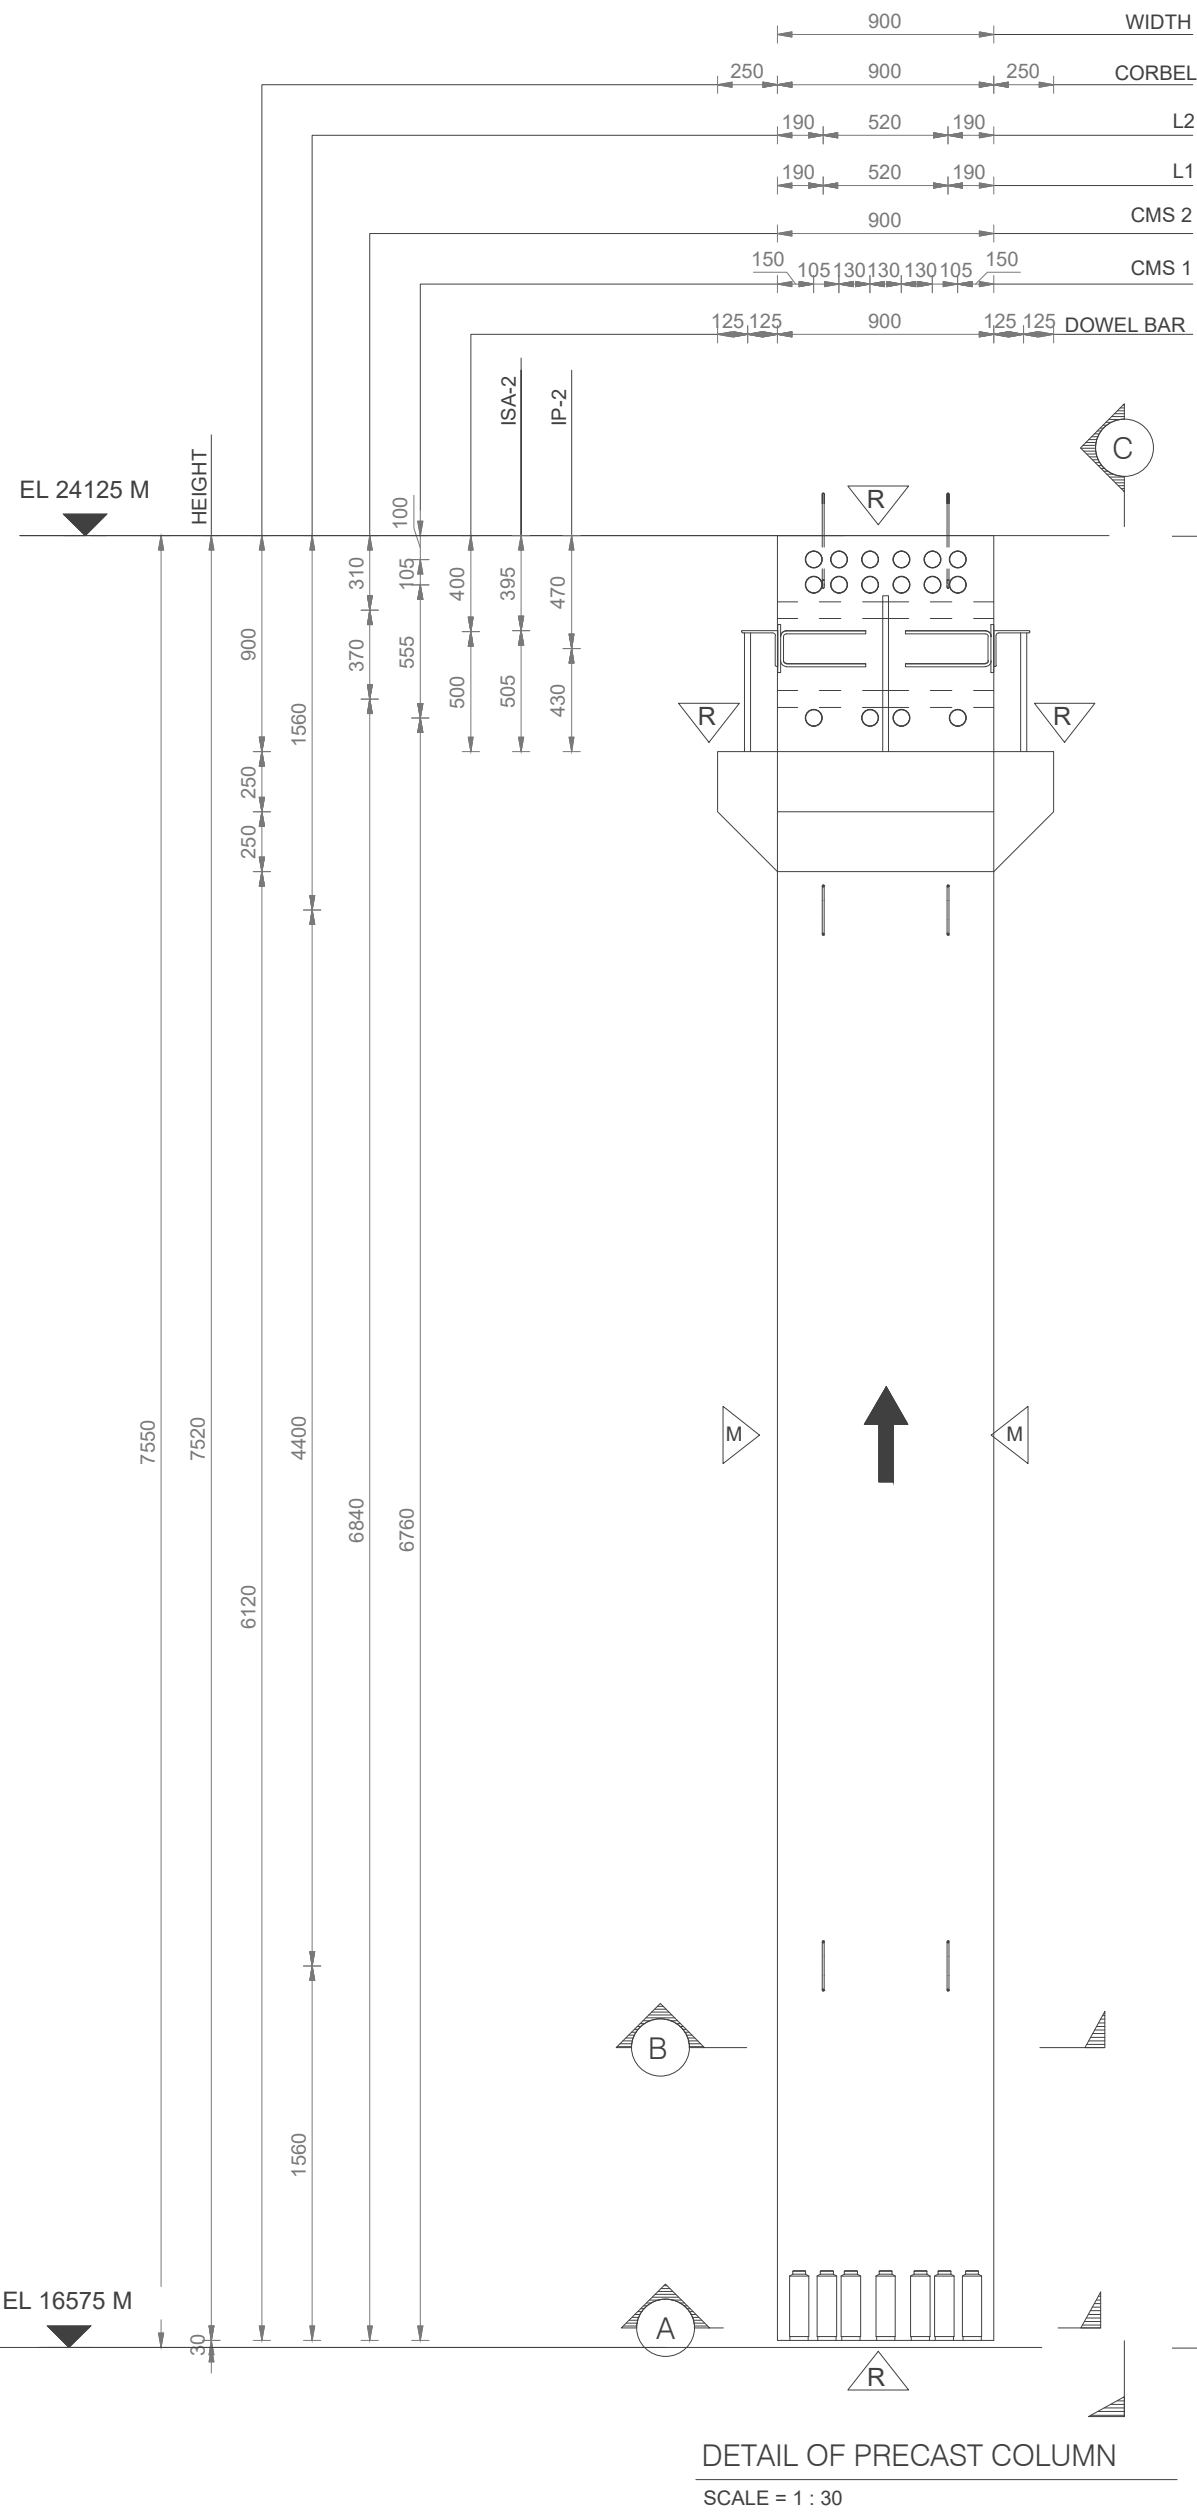


DETAIL OF PRECAST COLUMN
SCALE = 1 : 30

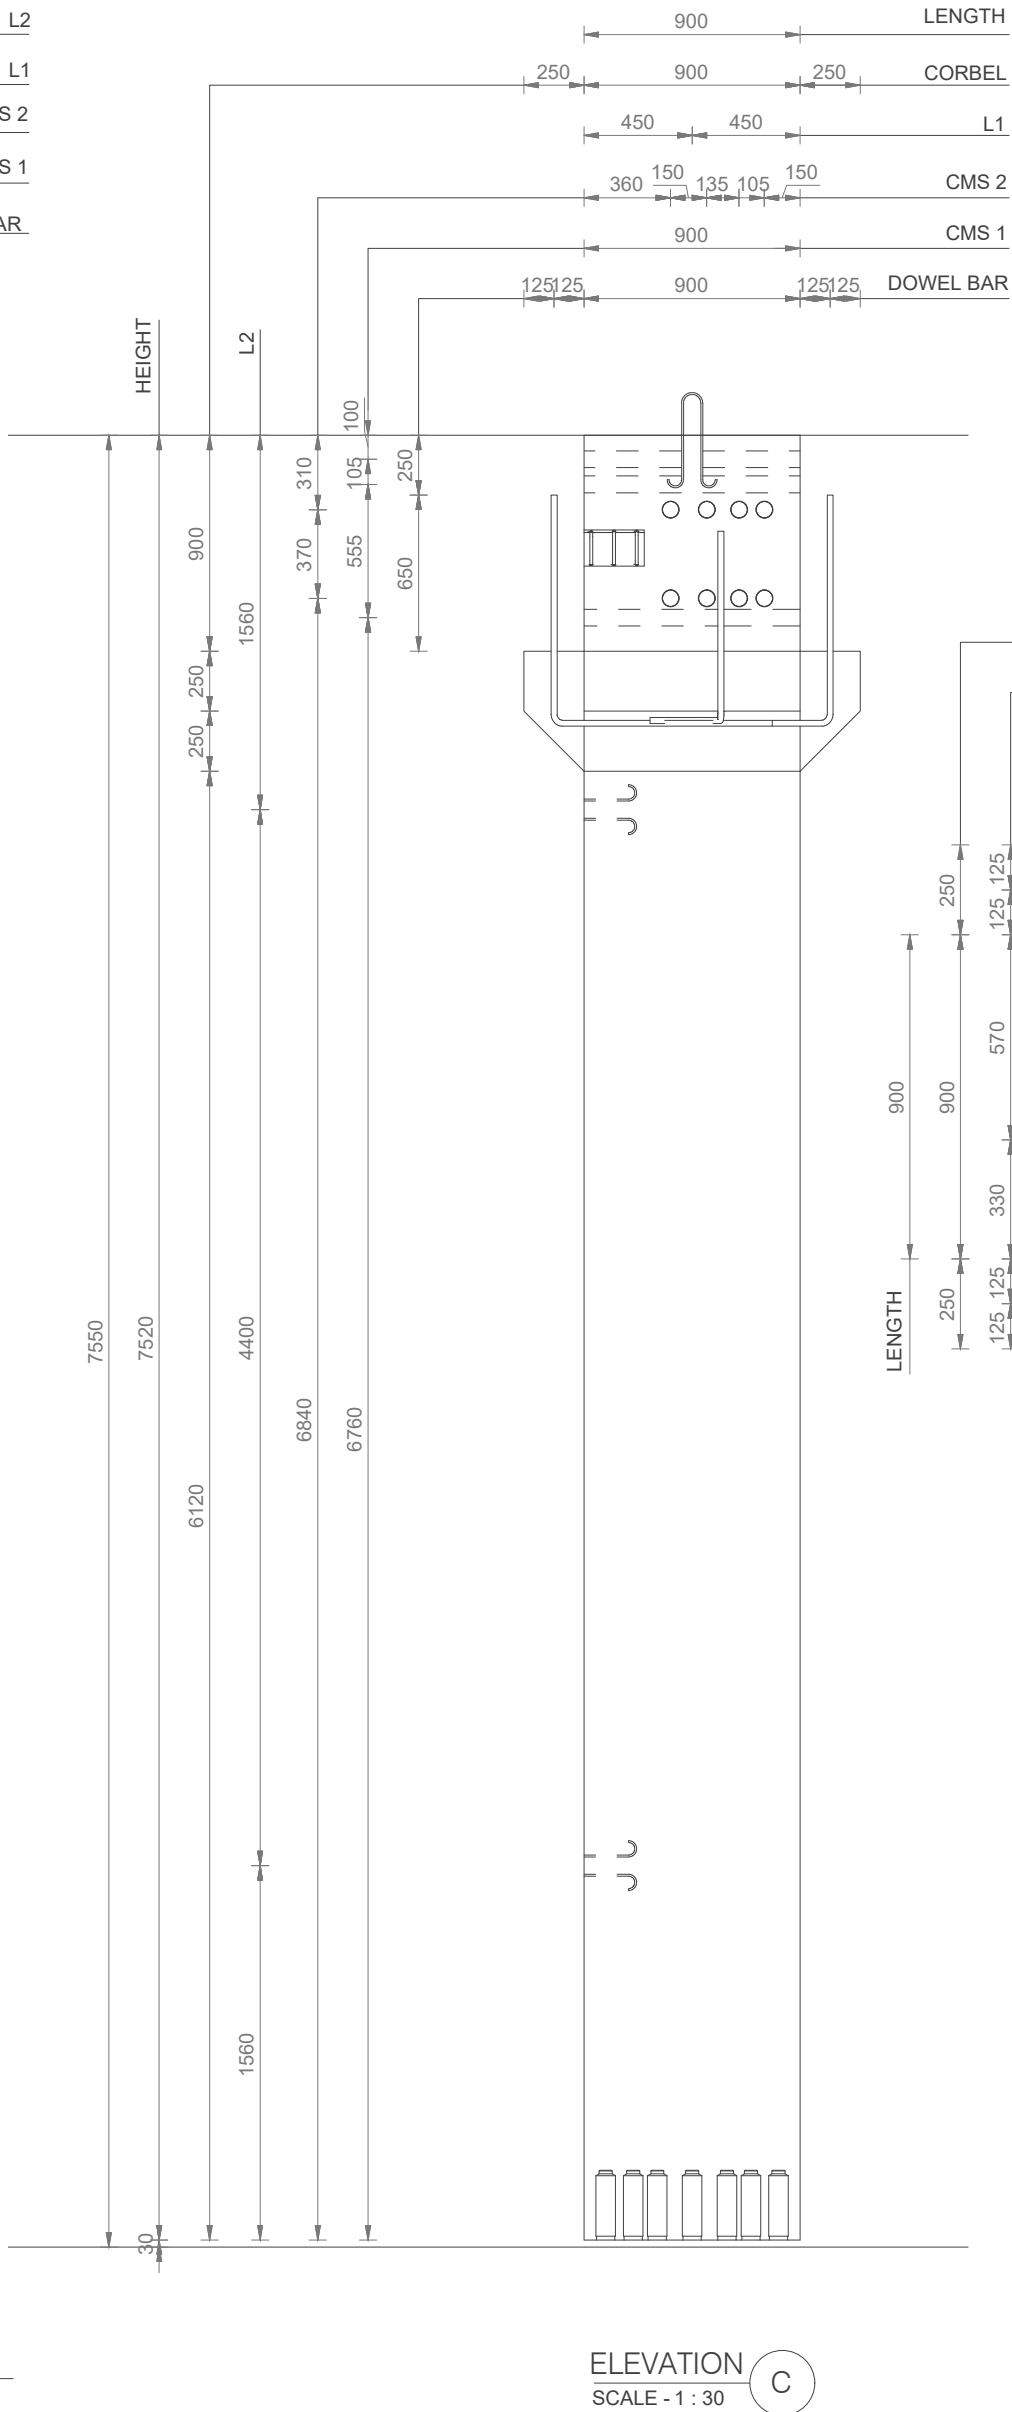

ELEVATION
SCALE - 1 : 30

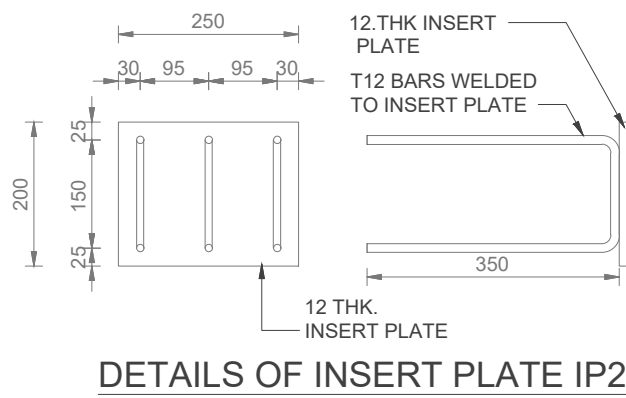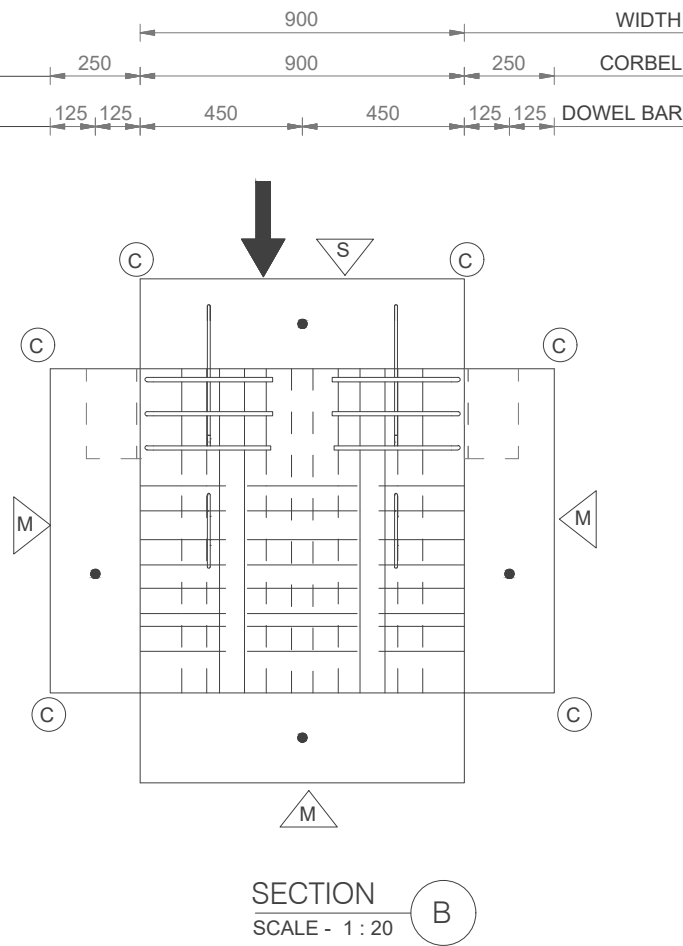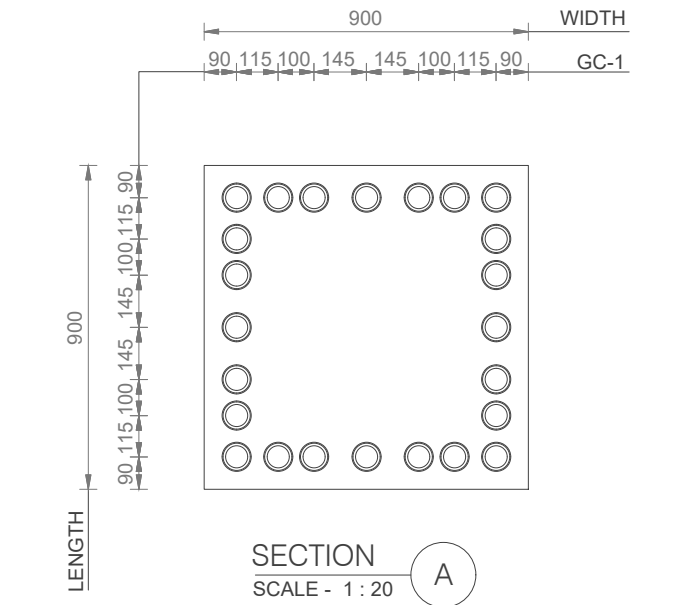

DETAILS OF IP2					
PLATE PROFILE	WT OF PLATE / IP IN KG	DIA OF LUGS	NO. OF LUGS / IP	TOTAL LENGTH OF LUGS / IP IN METER	TOTAL LUGS WEIGHT / IP IN KG
250X200X12	4.71	12	3	2.55	2.66

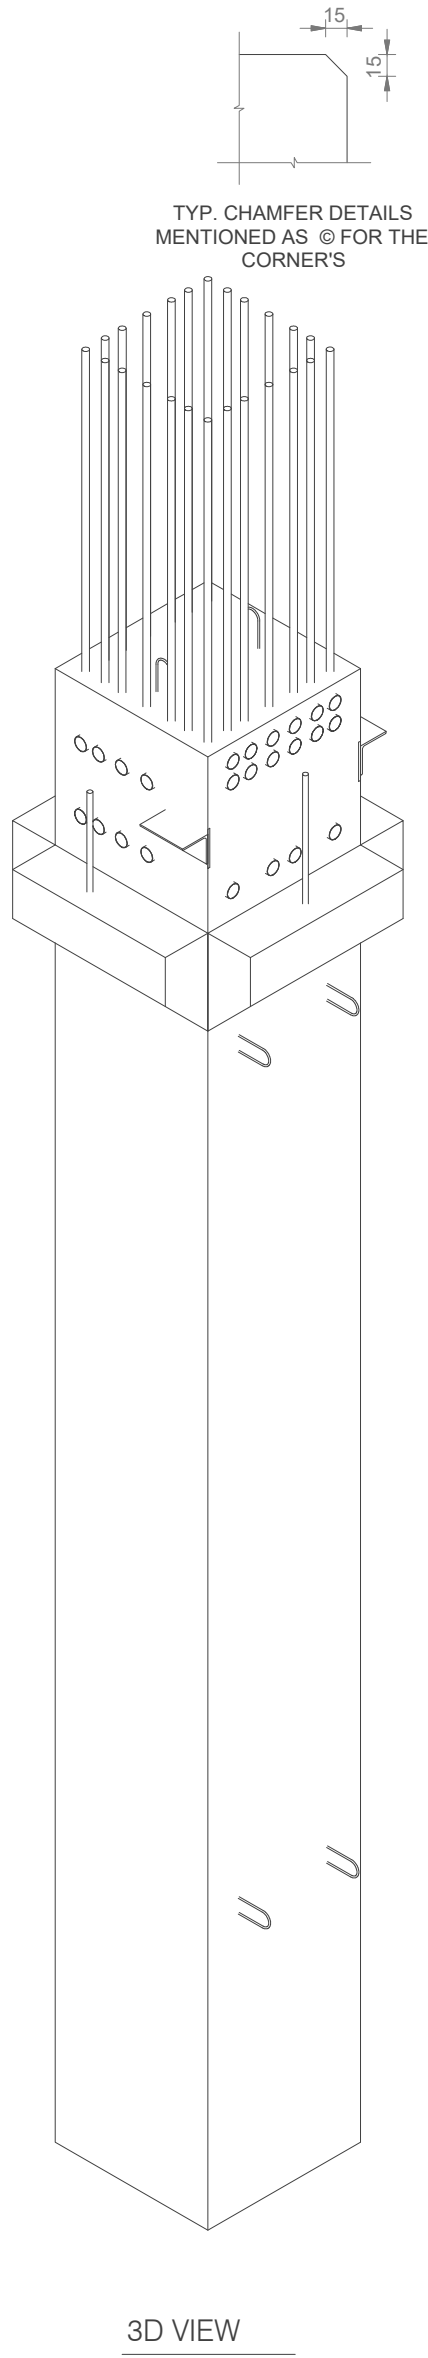

3D VIEW

LEGEND:-	
- RAKED SURFACE	- SMOOTH FINISH
- MOULD FINISH	- CHAMFER 15x15
- ERECTION MARK / VIEW DIRECTION	
NOTES:	
1. ALL DIMENSIONS ARE IN MM AND FOLLOW WRITTEN DIMENSIONS, DO NOT MEASURE.	
2. CLEAR COVER FOR : A. PRECAST COLUMN = 60mm B. PRECAST COLUMN CORBEL = 30mm	
3. GRADE OF REINFORCING STEEL, Fe 550D -TMT BARS CONFORMING TO IS1786:2008 WITH MINIMUM YIELD STRENGTH OF 550 N/mm ²	
4. CONCRETE STRENGTH : A. AFTER 28 DAYS : @ M70 B. DEMOULDING & LIFTING : @ M20 C. TRANSPORTATION & ERECTION : @ M50	
DEMOULDING METHOD : HORIZONTAL	
STACKING METHOD : HORIZONTAL	
TRANSPORT METHOD : HORIZONTAL	
ERECTION METHOD : NO. OF LIFTER AS PER SHOP DRAWING	

Diagram illustrating the identification of a precast column. The central box is labeled **N3A-1-B1-1**. It is connected to four other boxes: **SITE NUMBER NMI3 / 4 / 5**, **FLOOR LEVEL**, **UNIQUE ID**, and **BUILDING DGA - A, DGB - B, DC - C**. An **ELEMENT MARK** box is also connected to the central box.

MARK	DESCRIPTION	QTY.
CMS-1	70 DIA PIC SLEEVE	16
CMS-2	70 DIA PIC SLEEVE	8
GC-1	Ø32 GROUTC COUPLER 'L' TYPE	24
IP-2	250X200X12 THK. PLATE	2
ISA-2	ISA150x150x10	2
L1	LIFTER-15 TON CAPACITY EACH	2
L2	LIFTER-10 TON CAPACITY EACH	4
Grand total: 58		

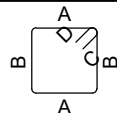
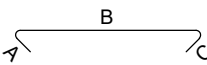
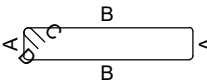
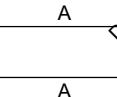
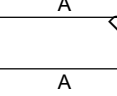
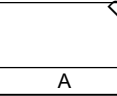
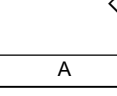
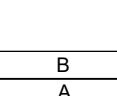
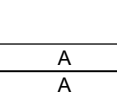
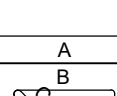
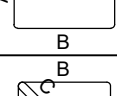
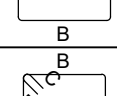
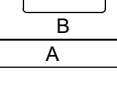
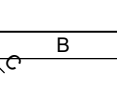
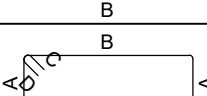
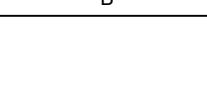
PRECAST COLUMN VOLUME (M ³)	PRECAST COLUMN WEIGHT (TONNES)
6.36	16.85















Diagram illustrating a typical lifter detail. A precast column is shown with a GI pipe (optional) and 12.9Ø strands. The diagram includes dimensions: 0.51m for the top section, R=50 for the curve, and E1 for the vertical section. The column is labeled **PRECAST COLUMN**.

TYPICAL LIFTER DETAIL

(REFER STANDARRD LIFTING DETAILS DRAWING FOR LIFTER CAPACITY)

REFERENCE DRAWING						
DRAWING NO.		DESCRIPTION				
N3C-2-C18 -RF		REINFORCEMENT DETAILS OF PRECAST COLUMN -N3C-2-C18				
N3C-2-C18 -RF1		REINFORCEMENT DETAILS OF PRECAST COLUMN -N3C-2-C18				
R0	02-07-2026	GOOD FOR CONSTRUCTION	SPS	SAM	SDK	
REV.	DATE	DRAWING STATUS	DRAWN BY	CHECKED BY	APPROVED BY	
REVISION HISTORY						
STRUCTURAL CONSULTANT :		PPS ENGINEERING CONSULTANTS LLP.				
		FIRST FLOOR, SERVICE BUILDING, BAFI BHAVAN, DR. MANISHAI DESAI NAGAR, WARJE, PUNE 411058, INDIA. EMAIL : design@ppspl.in WEB SITE : www.ppspl.in Tel. : + 91 20 25232858				
PROJECT NUMBER		25-4035				
PROJECT NAME		ACXNMI-03				
 Your Growth. Our Priority.		CLIENT ADANICONNEX				
DETAILS OF PRECAST COLUMN : N3C-2-C18						
DWG NUMBER		N3C-2-C18-F				
RELEASED FOR	APPROVAL		NAME	DATE	SCALE : AS SHOWN SIZE : A2 REV. : R0	
	TENDER		DRAWN	SPS		02-07-2026
	CONSTRUCTION	✓	CHECKED	SAM		02-07-2026
	INFORMATION		APPROVED	SDK		02-07-2026

N3C-2-C18 REBAR SCHEDULE												
BENDING DIMENSIONS												
BAR MARK	BAR DIAMETER	QTY.	BENDING DETAILS	A	B	C	C1	D	D1	BAR CUTTING LENGTH	TOTAL BAR LENGTH	TOTAL WEIGHT
261	10	8		840	0	0		0		840	6800	4.20 kg
622	12	72		780	780	96		96		3253	235800	209.61 kg
1199	10	216		80	780	80		0		940	205200	126.67 kg
2031	10	252		155	780	80		80		1981	504000	311.13 kg
5402	10	1		840	260	80		80		2310	2325	1.44 kg
5616	10	1		840	262	80		80		2315	2325	1.44 kg
5710	10	1		840	333	80		80		2456	2475	1.53 kg
5716	10	2		840	285	80		80		2361	4750	2.93 kg
6101	25	5		202	1310	202		300		1633	8250	31.83 kg
6102	10	1		840	333	80		80		2455	2475	1.53 kg
6103	10	1		840	379	80		80		2549	2550	1.57 kg
6125	10	2		816	1255	80		80		4251	8550	5.28 kg
6126	10	2		815	1147	80		80		4034	8100	5.00 kg
6129	10	2		816	1024	80		80		3790	7600	4.69 kg
6184	25	2		963	963	0		0		1884	3800	14.66 kg
6187	10	2		421	1024	80		80		3001	6050	3.73 kg
6189	10	2		421	1255	80		80		3462	6950	4.29 kg

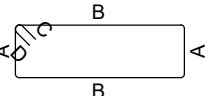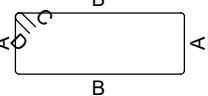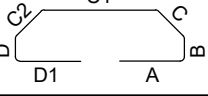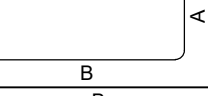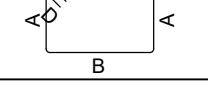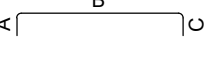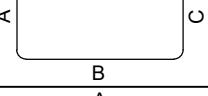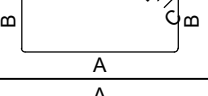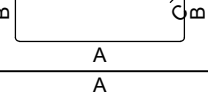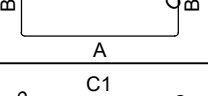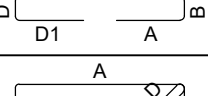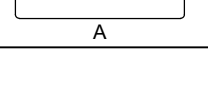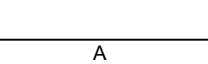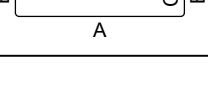N3C-2-C18 REBAR SCHEDULE												
BENDING DIMENSIONS												
BAR MARK	BAR DIAMETER	QTY.	BENDING DETAILS	A	B	C	C1	D	D1	BAR CUTTING LENGTH	TOTAL BAR LENGTH	TOTAL WEIGHT
6196	10	6		423	1339	80		80		3633	21900	13.52 kg
6197	10	2		423	1147	80		80		3250	6500	4.01 kg
6226	12	5		482	186	286	851	189	484	2698	13500	12.00 kg
6546	25	2		802	963	0		0		1723	3450	13.31 kg
6580	10	6		815	1339	80		80		4418	26550	16.39 kg
6610	10	6		80	828	80		0		955	5850	3.61 kg
6953	10	1		840	381	80		80		2553	2575	1.59 kg
7375	25	5		178	1314	178		300		1588	8000	30.87 kg
7381	10	1		840	355	80		80		2501	2525	1.56 kg
7384	10	1		840	303	80		80		2397	2400	1.48 kg
7385	10	1		840	354	80		80		2499	2500	1.54 kg
7386	12	5		506	160	303	826	163	507	2703	13625	12.11 kg
7387	10	1		840	310	80		80		2409	2425	1.50 kg
8107	32	24		8895	0	0		0		8895	213600	1375.68 kg
8113	12	3		828	828	96		96		3405	10275	9.13 kg
8133	10	12		828	205	80		80		2144	25800	15.93 kg
653											1379475	2245.77 kg

N3C-2-C18 REBAR SCHEDULE SUMMARY		
BAR DIAMETER	TOTAL BAR LENGTH	TOTAL WEIGHT
10	869175	536.56 kg
12	273200	242.86 kg
25	23500	90.67 kg
32	213600	1375.68 kg
1379475		2245.77 kg

R0	02-07-2026	GOOD FOR CONSTRUCTION	SPS	SAM	SDK
REV.	DATE	DRAWING STATUS	DRAWN BY	CHECKED BY	APPROVED BY
REVISION HISTORY					
STRUCTURAL CONSULTANT :		PPS ENGINEERING CONSULTANTS LLP.			
		FIRST FLOOR, SERVICE BUILDING, BAIF BHAVAN, DR. MANIBHAI DESAI NAGAR, WAKURJE, PUNE-411058, INDIA. EMAIL : design@ppsepl.in WEB SITE : www.ppsepl.in Tel. : + 91 20 25232558			
PROJECT NUMBER		25-4035			
PROJECT NAME		ACXNMI-03			
		CLIENT			
		ADANICONNEX			
REINFORCEMENT DETAILS OF PRECAST COLUMN :		N3C-2-C18			
DWG NUMBER		N3C-2-C18-RF1			
RELEASED BY	APPROVAL		NAME	DATE	SCALE : AS SHOWN REV : R0
	TENDER		SPS	02-07-2026	
	CONSTRUCTION	✓	CHECKED	SAM	
	INFORMATION		APPROVED	SDK	
				02-07-2026	
		SIZE : A2			