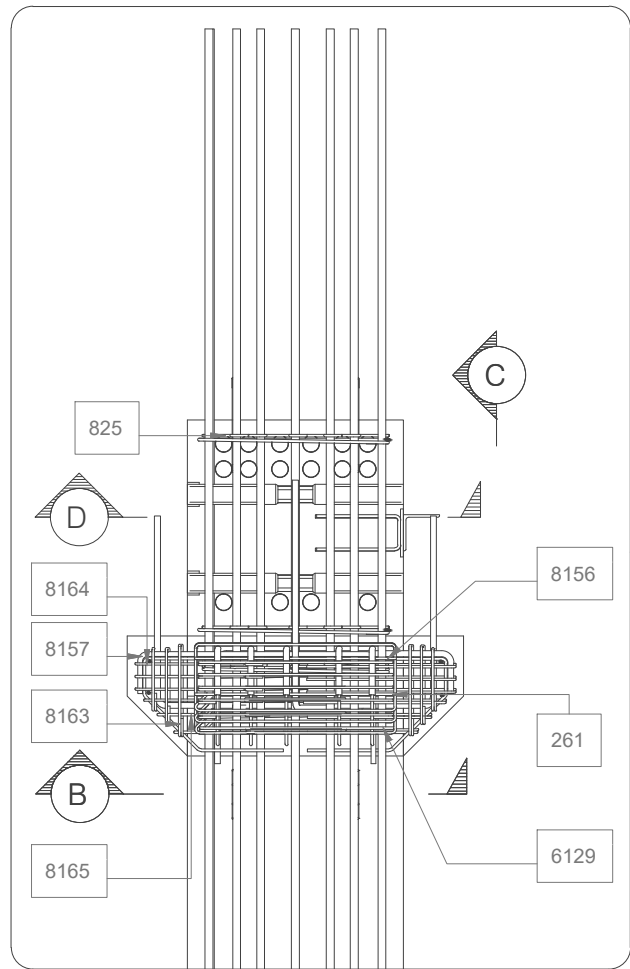
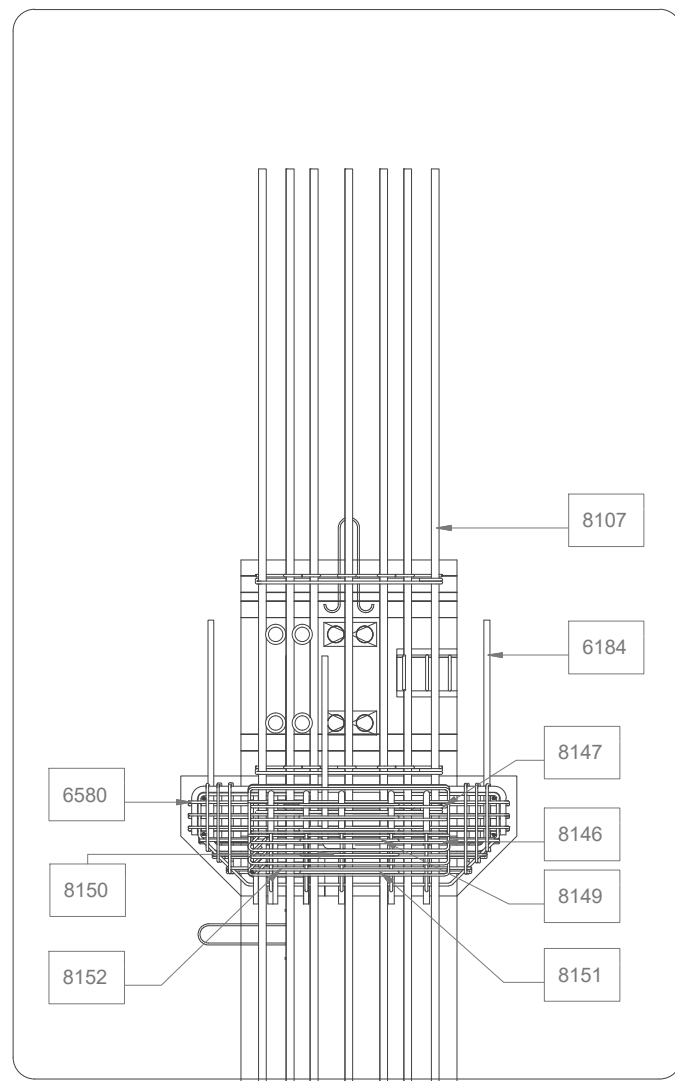


7520
6453
T10 @100 C/C (2155)
7309
T12 @100 C/C (7382)
208
T10 @100 C/C (6919)
211
T12 @100 C/C (6609)
30



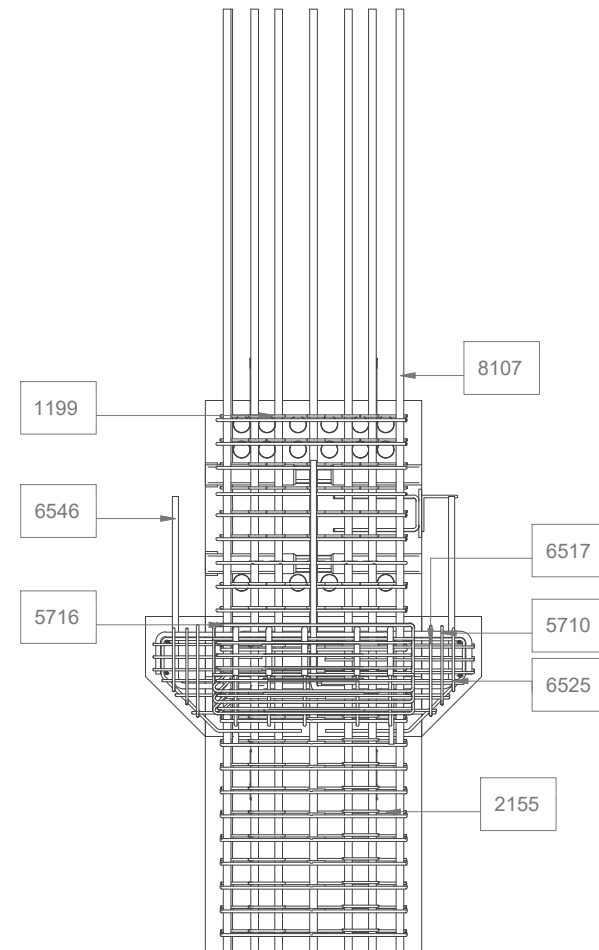
REINFORCEMENT DETAILS OF PRECAST COLUMN
SCALE = 1 : 30

1630
7520
24-T32(8091) 30




ELEVATION
SCALE - 1 : 30


2
N3C-2-C129-RF




DETAIL
SCALE - 1 : 30

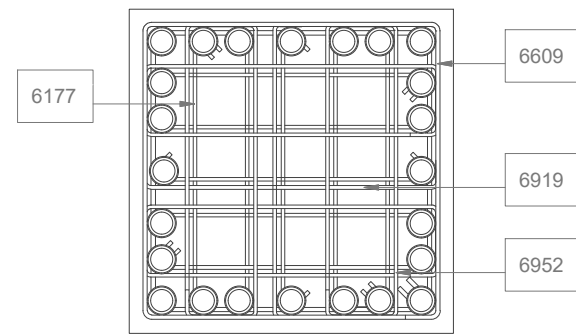


SECTION
SCALE - 1 : 20

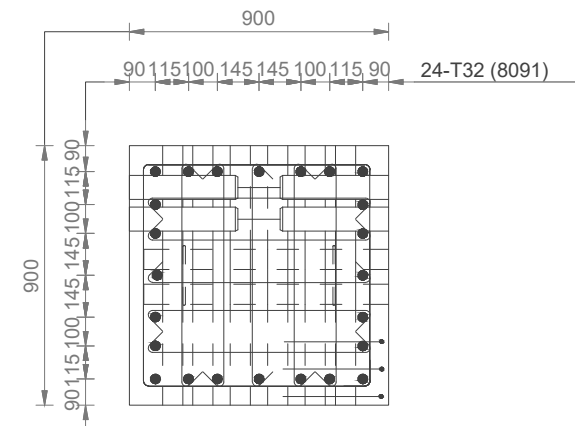

SECTION
SCALE - 1 : 25

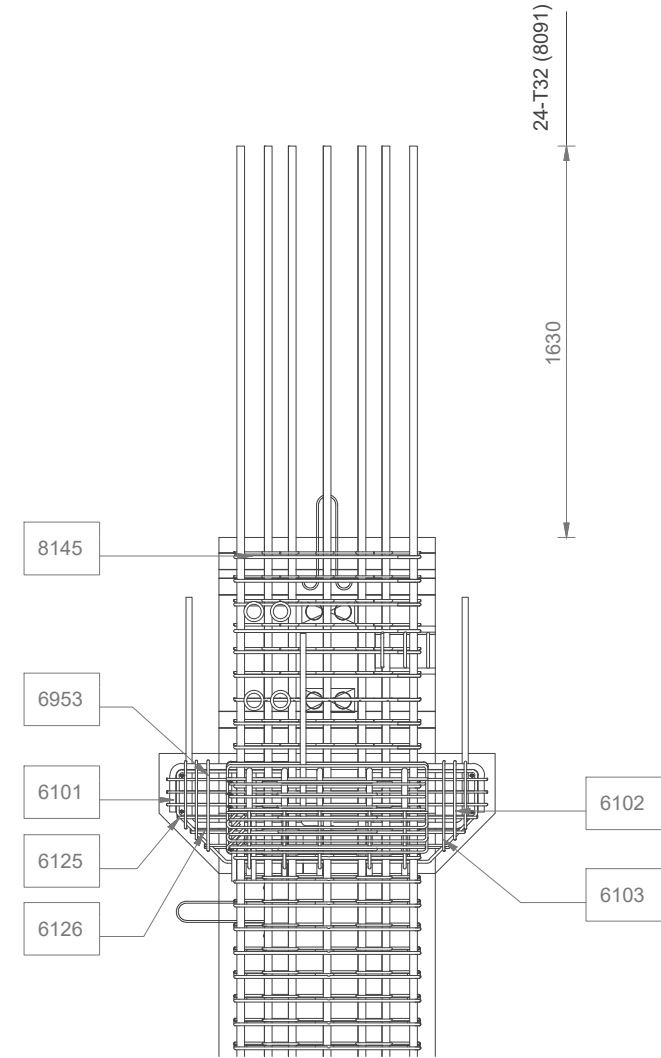


DETAIL
SCALE - 1 : 30

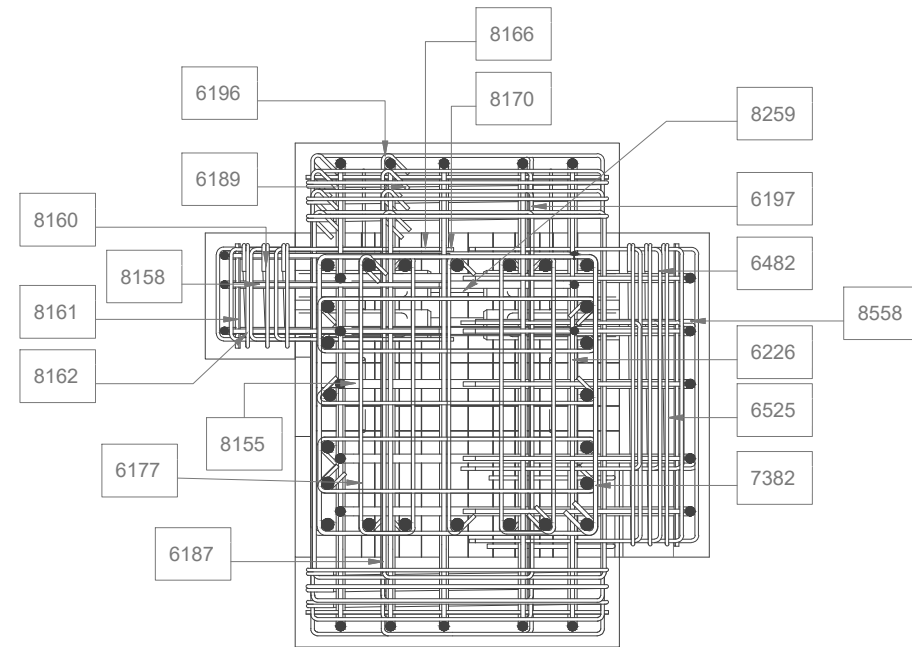


SECTION
SCALE - 1 : 20

R0	22-06-2026	GOOD FOR CONSTRUCTION	YRR	SAM	SDK
REV.	DATE	DRAWING STATUS	DRAWN BY	CHECKED BY	APPROVED BY
REVISION HISTORY					
STRUCTURAL CONSULTANT:		PPS ENGINEERING CONSULTANTS LLP.			
PPS		FIRST FLOOR, SERVICE BUILDING, BAFI BHAVAN, DR. MANISHAI DESAI NAGAR, WARJE, PUNE 411058, INDIA. EMAIL : design@ppspl.in			
		WEB SITE : www.ppspl.in Tel. : + 91 20 25232858			
PROJECT NUMBER		25-4035			
PROJECT NAME		ACXNMI-03			
CLIENT		ADANICONNEX			
REINFORCEMENT DETAILS OF PRECAST COLUMN :		N3C-2-C129			
DWG NUMBER		N3C-2-C129-RF			
REVIEWED FOR	APPROVAL		NAME	DATE	SCALE : AS SHOWN SIZE : A2 REV. : R0
	TENDER		DRAWN	YRR	
	CONSTRUCTION	✓	CHECKED	SAM	
	INFORMATION		APPROVED	SDK	

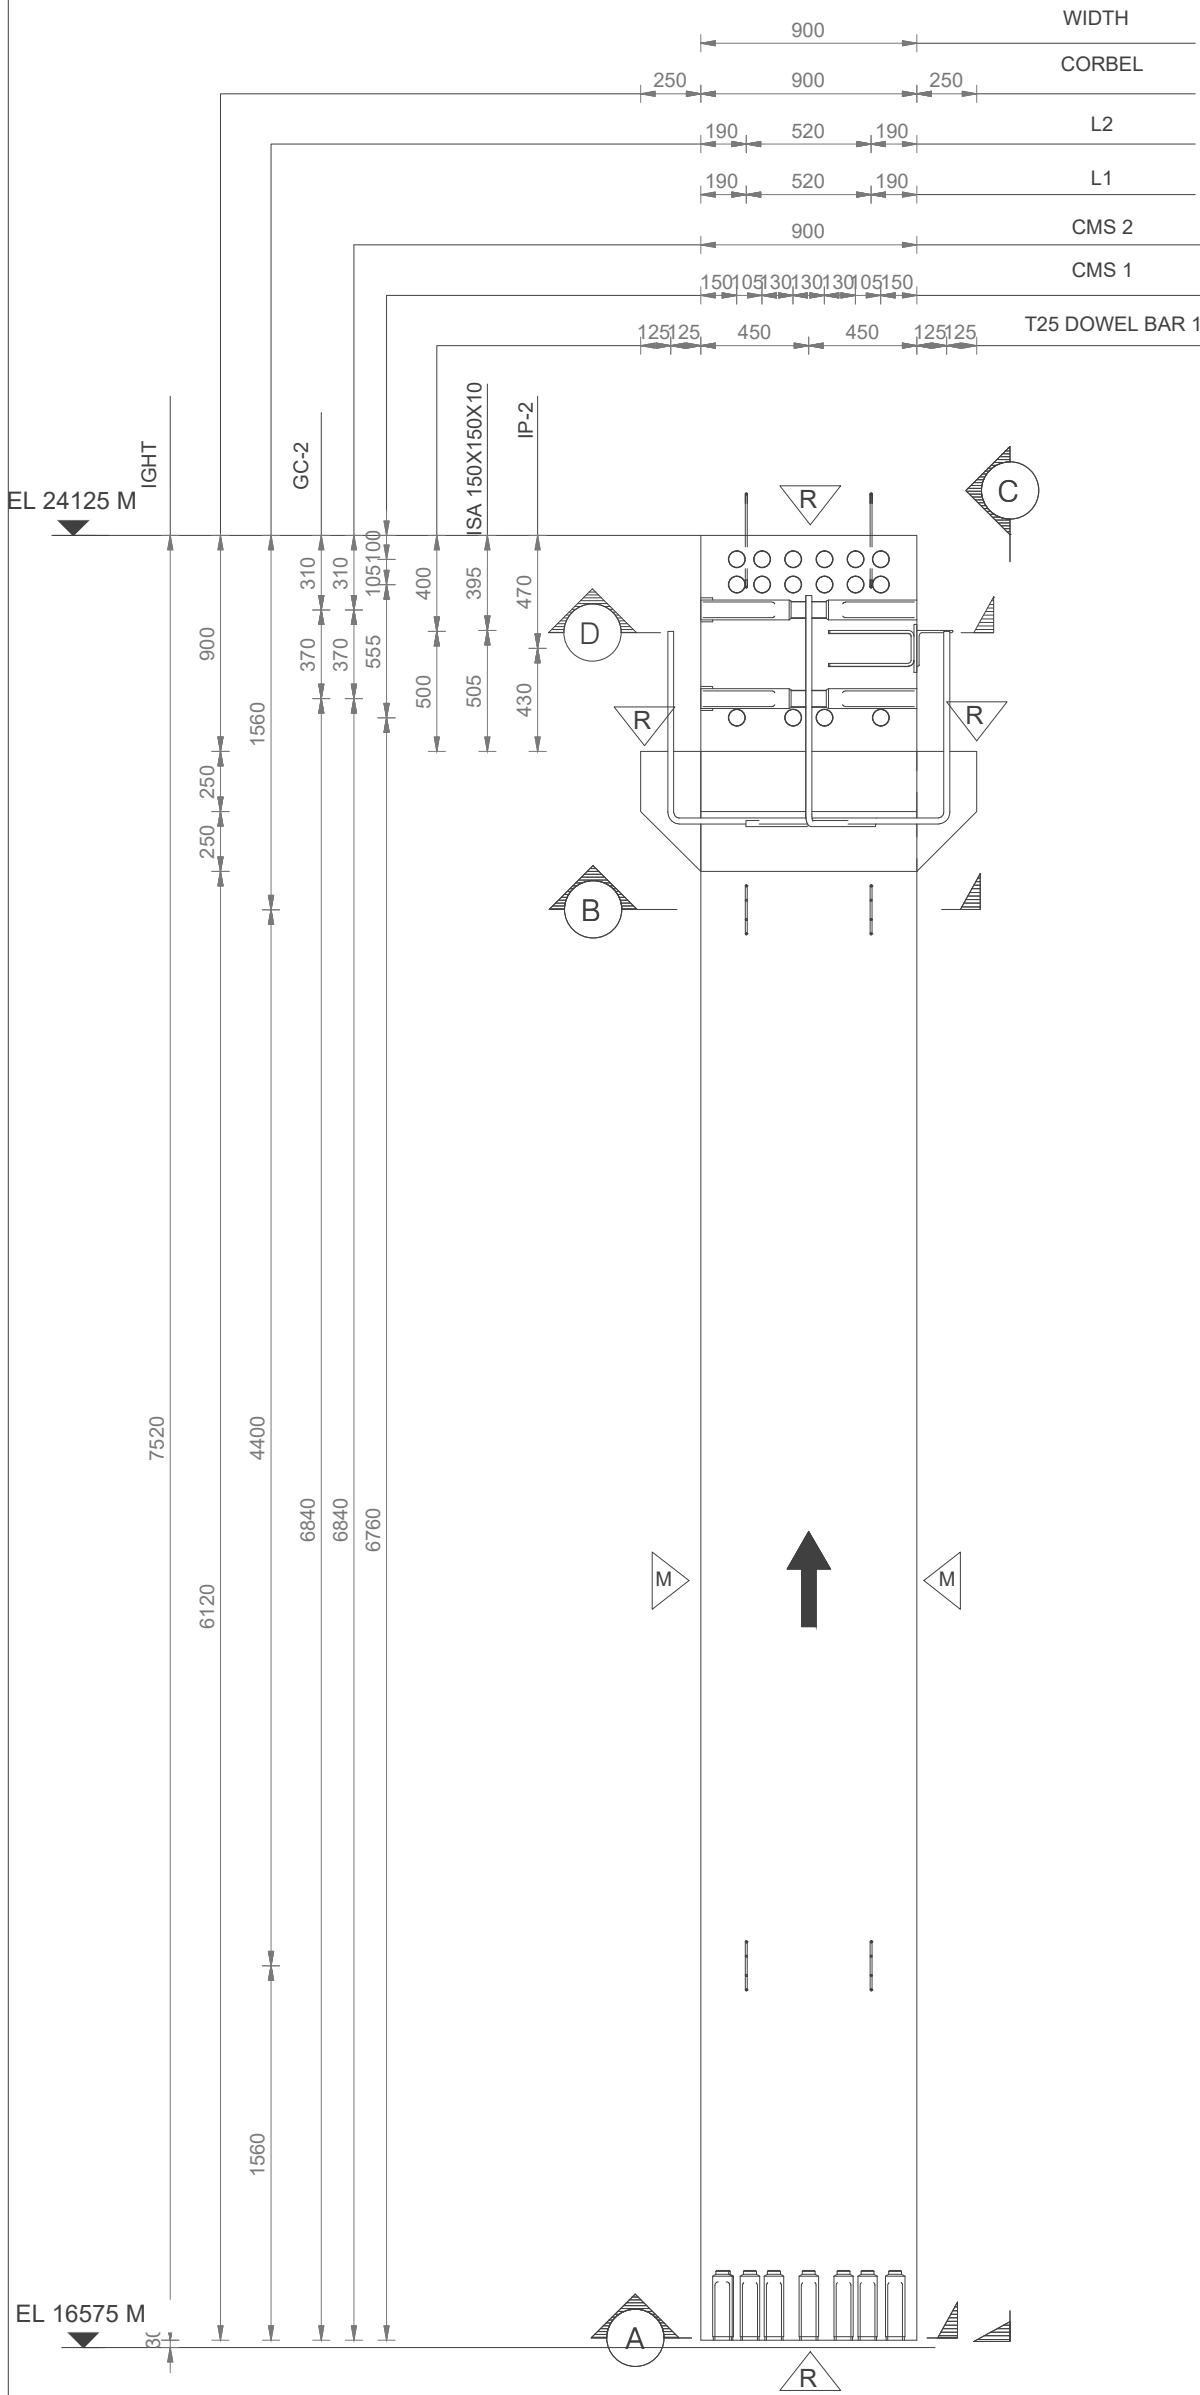


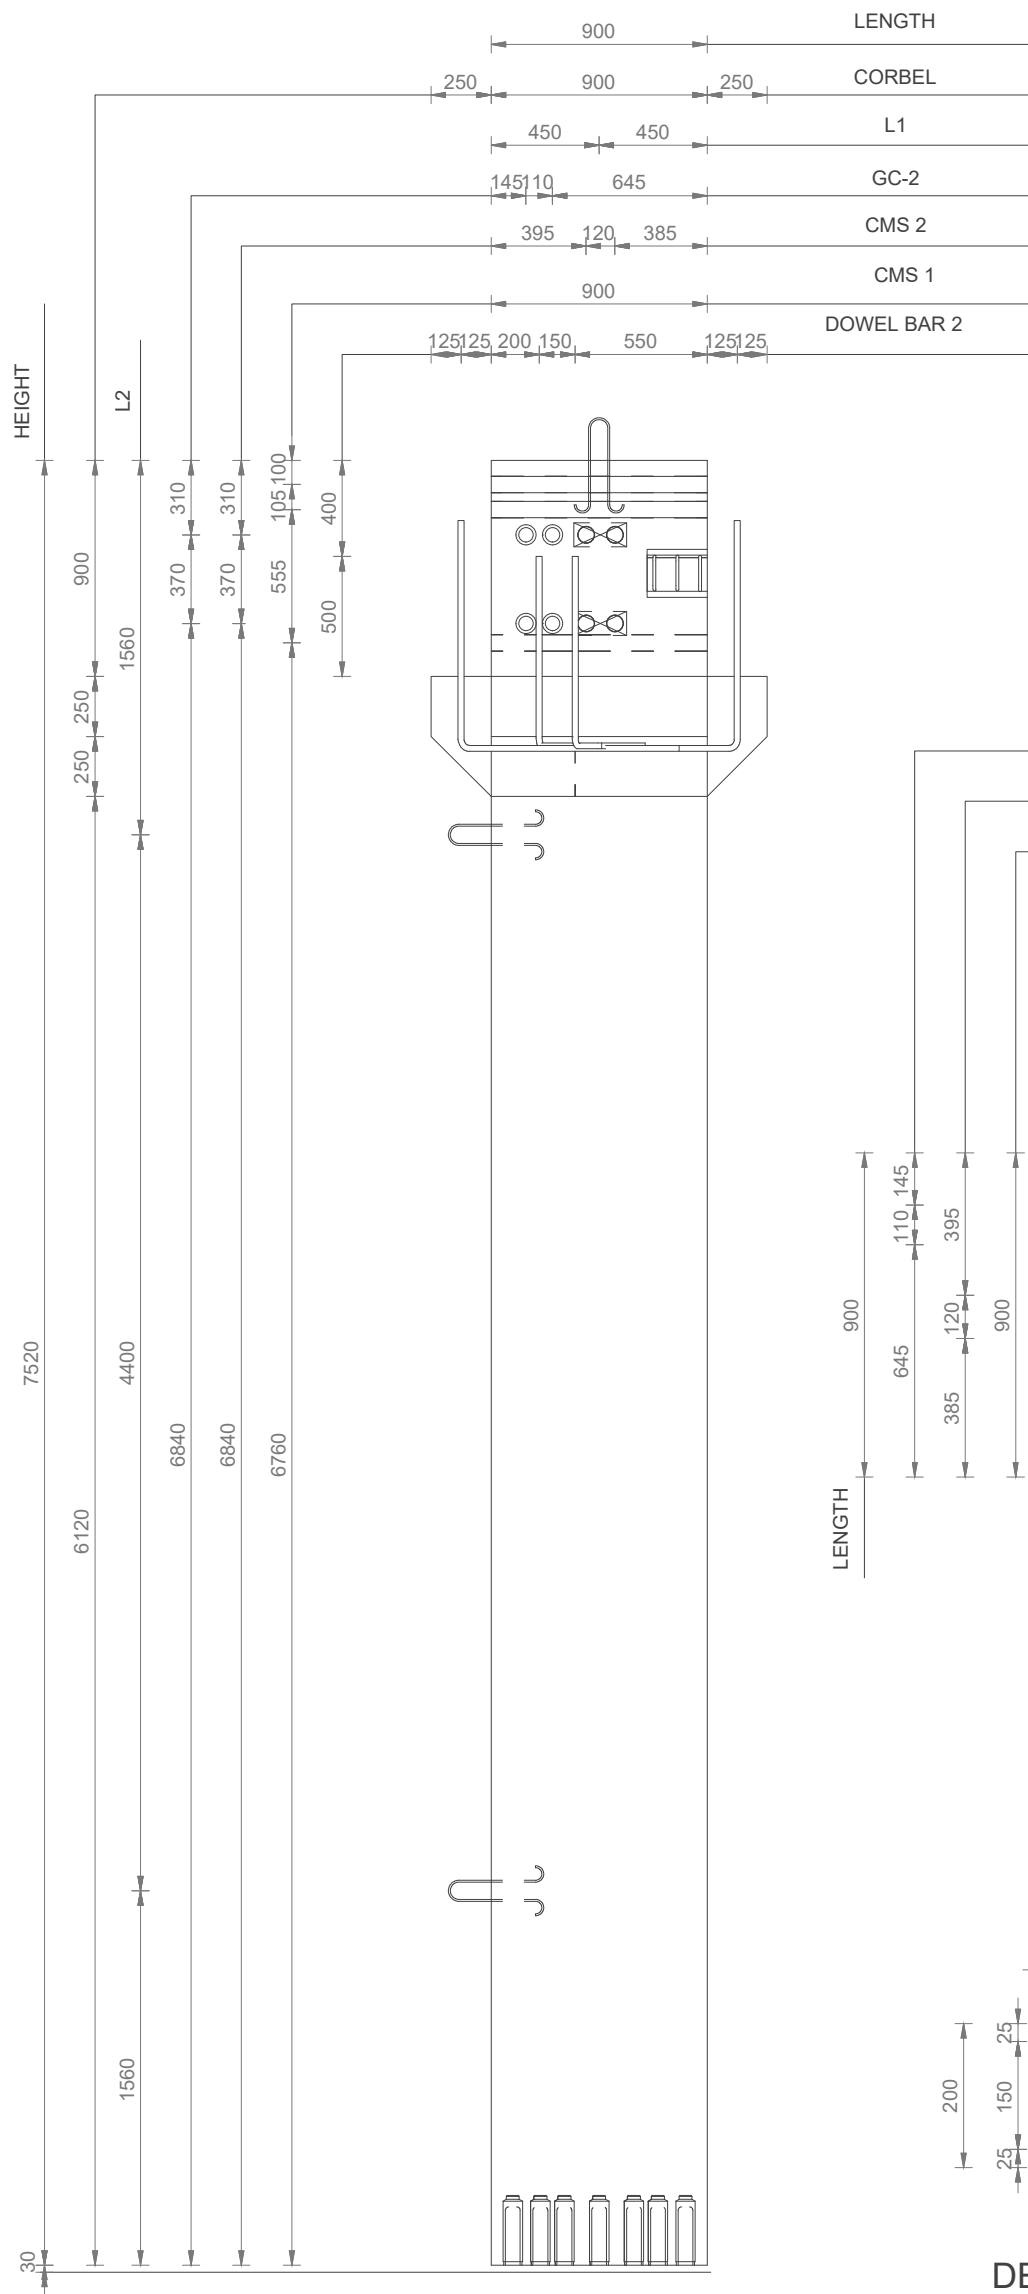
DETAILS OF PRECAST COLUMN
SCALE = 1 : 30




ELEVATION
SCALE - 1 : 30

DETAILS OF INSERT PLATE IP1


DETAILS OF IP1					
PLATE PROFILE	WT OF PLATE / IP IN KG	DIA OF LUGS	NO. OF LUGS / IP	TOTAL LENGTH OF LUGS / IP IN METER	TOTAL LUGS OF LUGS / IP IN KG
150X200X12	2.82	12	2	1.80	1.80

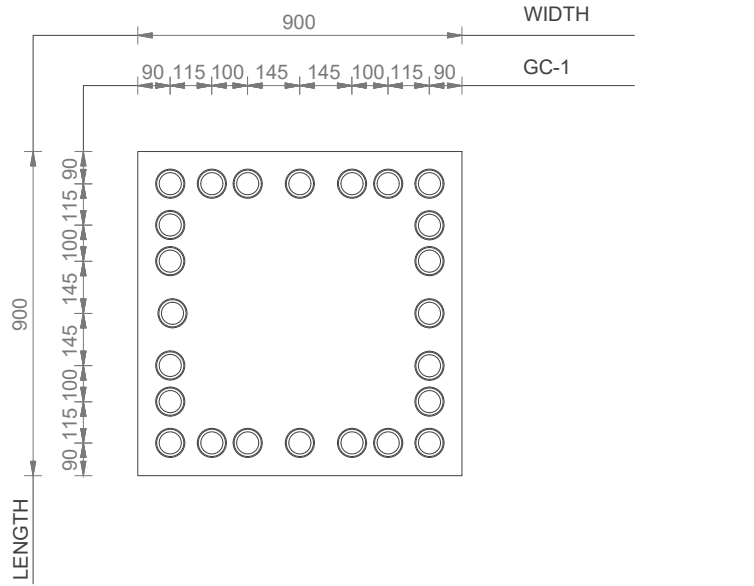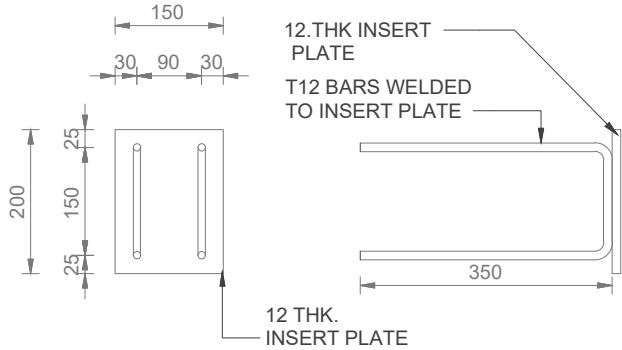


SECTION A
SCALE - 1 : 20

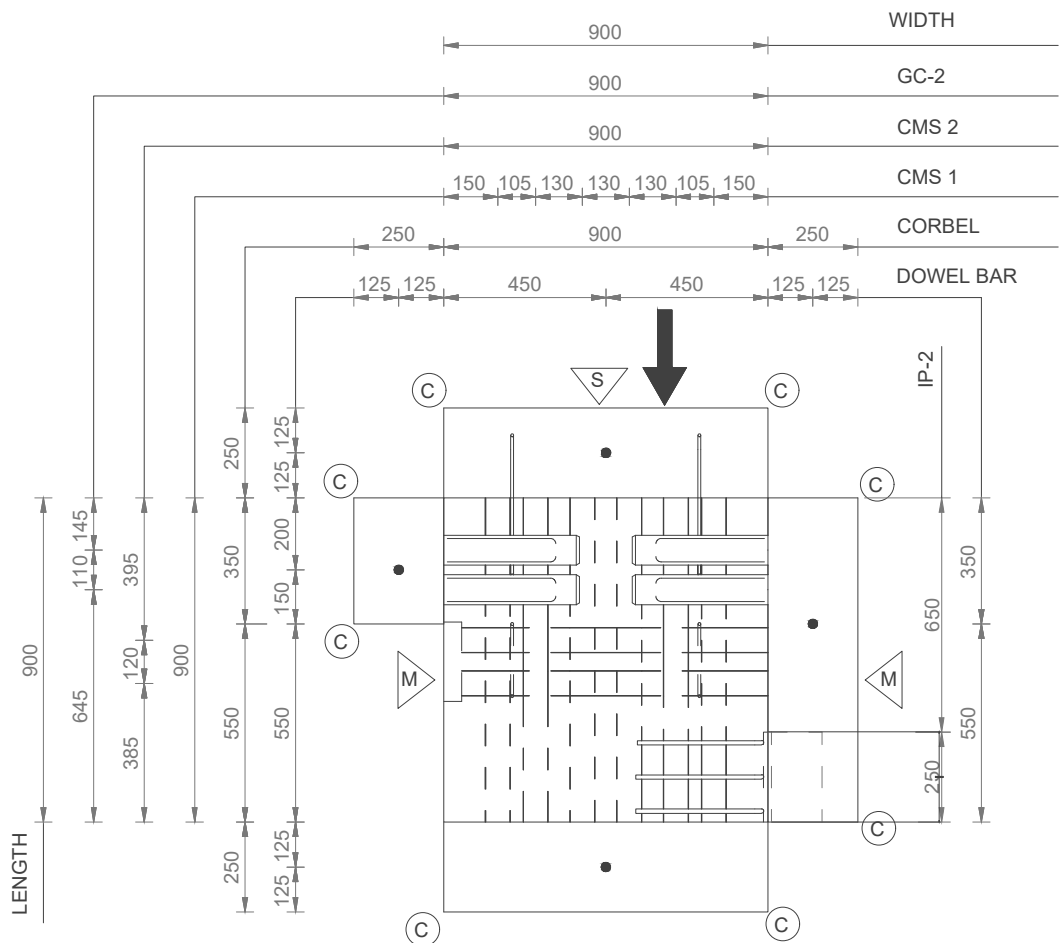

SECTION B
SCALE - 1 : 20

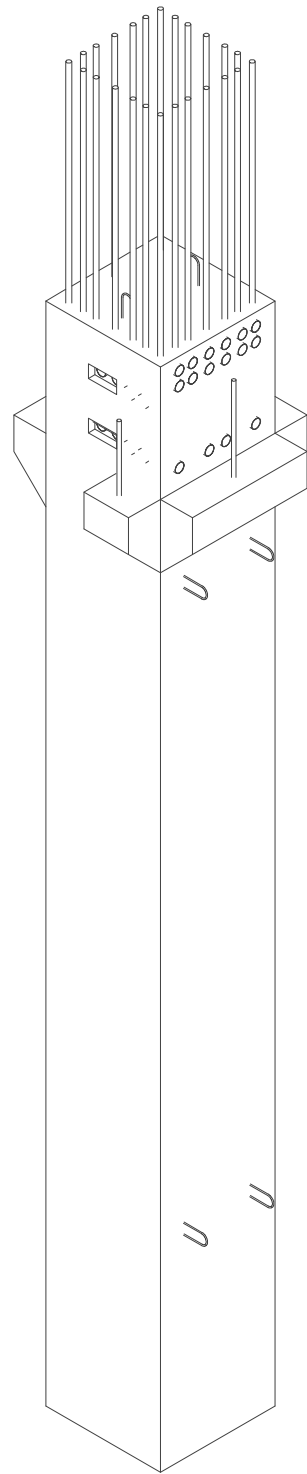

3D VIEW

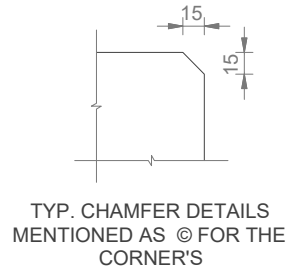

TYP. CHAMFER DETAILS
MENTIONED AS @ FOR THE
CORNER'S


LEGEND:-

- R - RAKED SURFACE
- S - SMOOTH FINISH
- M - MOULD FINISH
- C - CHAMFER 15x15
- ERECTION MARK / VIEW DIRECTION

NOTES:


- ALL DIMENSIONS ARE IN MM AND FOLLOW WRITTEN DIMENSIONS, DO NOT MEASURE.
- CLEAR COVER FOR :
 - A. PRECAST COLUMN = 60mm
 - B. PRECAST COLUMN CORBEL = 30mm
- GRADE OF REINFORCING STEEL, Fe 550D -TMT BARS CONFORMING TO IS1786:2008 WITH MINIMUM YIELD STRENGTH OF 550 N/mm²
- CONCRETE STRENGTH :
 - A. AFTER 28 DAYS : @ M70
 - B. DEMOULDING & LIFTING : @ M20
 - C. TRANSPORTATION & ERECTION : @ M50

DEMOLDING METHOD : HORIZONTAL	
STACKING METHOD	: HORIZONTAL
TRANSPORT METHOD	: HORIZONTAL
ERECTION METHOD	: NO. OF LIFTER AS PER SHOP DRAWING

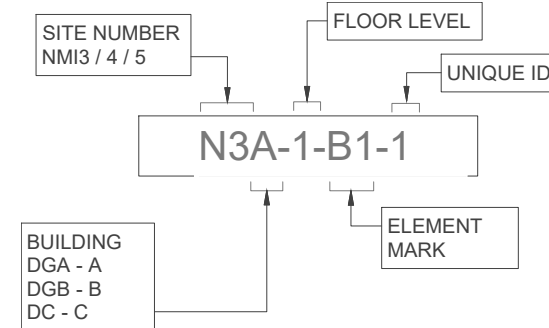

MARK	DESCRIPTION	QTY.
CMS-1	70 DIA PIC SLEEVE	16
CMS-2	70 DIA PIC SLEEVE	4
GC-1	Ø32 GROUT COUPLER 'L' TYPE	24
GC-2	Ø40 GROUT COUPLER 'S' TYPE	8
IP-2	250X200X12 THK. PLATE	1
ISA-1	ISA150x150x10	1
L1	LIFTER-15 TON CAPACITY EACH	2
L2	LIFTER-10 TON CAPACITY EACH	4
Grand total: 60		

PRECAST COLUMN VOLUME (M ³)	PRECAST COLUMN WEIGHT (TONNES)
6.32	16.74

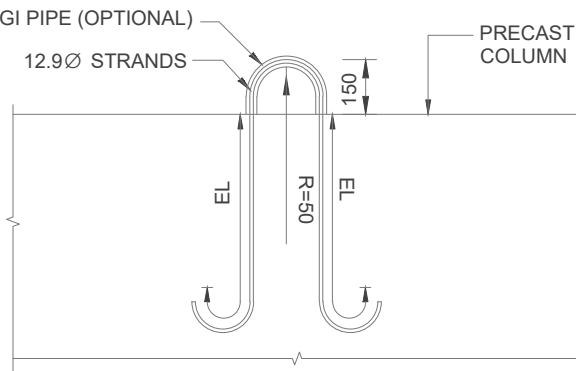

TYPICAL LIFTER DETAIL

(REFER STANDARRD LIFTING DETAILS
DRAWING FOR LIFTER CAPACITY)

REFERENCE DRAWING

DRAWING NO.	DESCRIPTION
N3C-2-C129 -RF	REINFORCEMENT DETAILS OF PRECAST
N3C-2-C129 -RF1	REINFORCEMENT DETAILS OF PRECAST
COLUMN -N3C-2-C129	

REV.	DATE	DRAWING STATUS	DRAWN BY	CHECKED BY	APPROVED BY
R0	22-06-2026	GOOD FOR CONSTRUCTION	YRR	SAM	SDK














REVISION HISTORY	
STRUCTURAL CONSULTANT	PPS ENGINEERING CONSULTANTS LLP.
FIRST FLOOR, SERVICE BUILDING, BAFI BHAVAN, DR. MANISHAI DESAI NAGAR, WARJE, PUNE 411058, INDIA. EMAIL : design@ppsppl.in	
WEB SITE : www.ppspl.in Tel. : + 91 20 25232858	









PROJECT NUMBER	25-4035
PROJECT NAME	ACXNMI-03
CLIENT	ADANICONNEX

DETAILS OF PRECAST COLUMN : N3C-2-C129

DWG NUMBER		N3C-2-C129-F				
RELEASED FOR	APPROVAL		NAME	DATE	SCALE : AS SHOWN	REV. : R0
	TENDER		DRAWN	YRR		
	CONSTRUCTION	✓	CHECKED	SAM	22-06-2026	
	INFORMATION		APPROVED	SDK	22-06-2026	

ELEMENT NO.	REQUIRED NO.
N3C-2-C129	01
TOTAL	01

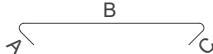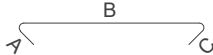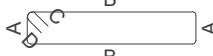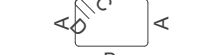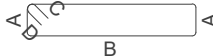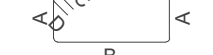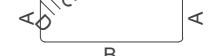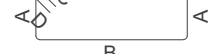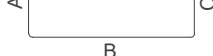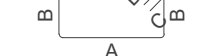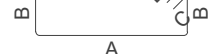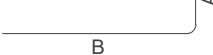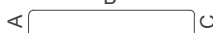N3C-2-C129 REBAR SCHEDULE											
			BENDING DIMENSIONS								
BAR MARK	BAR DIAMETER	QTY.	BENDING DETAILS	A	B	C	C1	D	BAR CUTTING LENGTH	TOTAL BAR LENGTH	TOTAL WEIGHT
261	10	6		840	0	0		0	840	5100	3.15 kg
825	10	108		80	780	80		0	940	102600	63.34 kg
1199	10	108		80	780	80		0	940	102600	63.34 kg
2155	10	189		155	775	80		80	1971	373275	230.43 kg
5710	10	2		840	332	80		80	2455	4950	3.06 kg
5716	10	2		840	285	80		80	2361	4750	2.93 kg
6101	25	5		202	1310	202		300	1633	8250	31.83 kg
6102	10	1		840	333	80		80	2455	2475	1.53 kg
6103	10	1		840	379	80		80	2549	2550	1.57 kg
6125	10	1		816	1255	80		80	4251	4275	2.64 kg
6126	10	1		815	1147	80		80	4034	4050	2.50 kg
6129	10	1		816	1024	80		80	3790	3800	2.35 kg
6177	10	63		155	778	80		80	1977	126000	77.78 kg
6184	25	2		963	963	0		0	1884	3800	14.66 kg
6187	10	1		421	1024	80		80	3001	3025	1.87 kg
6189	10	1		421	1255	80		80	3462	3475	2.15 kg
6196	10	3		423	1339	80		80	3633	10950	6.76 kg
6197	10	1		423	1147	80		80	3250	3250	2.01 kg
6226	12	5		482	186	286	851	189	2698	13500	12.00 kg
6482	10	1		518	820	518		300	1823	1825	1.13 kg
6517	10	1		840	381	80		80	2553	2575	1.59 kg
6525	10	1		840	267	80		80	2324	2325	1.44 kg
6546	25	2		802	963	0		0	1723	3450	13.31 kg
6580	10	3		815	1339	80		80	4418	13275	8.19 kg
6609	12	3		825	825	96		96	3393	10200	9.07 kg
6919	10	6		80	822	80		0	949	5700	3.52 kg

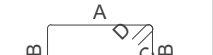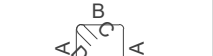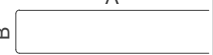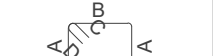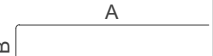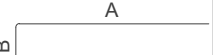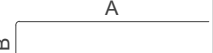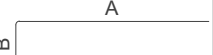N3C-2-C129 REBAR SCHEDULE											
			BENDING DIMENSIONS								
BAR MARK	BAR DIAMETER	QTY.	BENDING DETAILS	A	B	C	C1	D	BAR CUTTING LENGTH	TOTAL BAR LENGTH	TOTAL WEIGHT
6952	10	12		820	200	80		80	2118	25500	15.74 kg
6953	10	1		840	381	80		80	2553	2575	1.59 kg
7382	12	63		779	780	96		96	3252	206325	183.41 kg
8107	32	24		8895	0	0		0	8895	213600	1375.68 kg
8145	12	9		798	780	96		96	3250	29250	26.00 kg
8146	10	1		595	820	595		300	1977	2000	1.23 kg
8147	10	3		622	820	622		300	2032	6150	3.80 kg
8149	10	1		619	415	619		300	1620	1625	1.00 kg
8150	10	1		518	415	518		300	1418	1425	0.88 kg
8151	10	1		461	415	461		300	1303	1325	0.82 kg
8152	10	1		463	820	463		300	1713	1725	1.06 kg
8155	25	5		471	997	178		300	1564	7875	30.38 kg
8156	12	5		615	161	329	349	0	1424	7125	6.33 kg
8157	20	3		468	992	175		300	1569	4725	11.67 kg
8158	12	3		614	163	329	352	0	1427	4350	3.87 kg
8160	10	1		290	320	80		80	1331	1350	0.83 kg
8161	10	2		290	0	0		0	290	600	0.37 kg
8162	10	1		290	267	80		80	1224	1225	0.76 kg
8163	10	1		290	387	80		80	1464	1475	0.91 kg
8164	10	3		455	261	455		300	1139	3450	2.13 kg
8165	10	1		528	260	528		300	1283	1300	0.80 kg
8166	10	1		458	260	458		300	1144	1150	0.71 kg
8170	10	1		623	260	623		300	1473	1475	0.91 kg
8259	40	4		242	0	0		0	242	1000	9.88 kg
8558	10	3		619	419	619		300	1624	4875	3.01 kg
669									1355500	2247.91 kg	

N3C-2-C129 REBAR SCHEDULE SUMMARY		
BAR DIAMETER	TOTAL BAR LENGTH	TOTAL WEIGHT
10	842050	519.82 kg
12	270750	240.68 kg
20	4725	11.67 kg
25	23375	90.19 kg
32	213600	1375.68 kg
40	1000	9.88 kg
1355500		2247.91 kg

R0	22-06-2026	GOOD FOR CONSTRUCTION	YRR	SAM	SDK	
REV.	DATE	DRAWING STATUS	DRAWN BY	CHECKED BY	APPROVED BY	
REVISION HISTORY						
STRUCTURAL CONSULTANT :		PPS ENGINEERING CONSULTANTS LLP.				
		FIRST FLOOR, SERVICE BUILDING, BAFI BHAVAN, DR. MANIBHAI DESAI NAGAR, WARJE, PUNE 411058, INDIA. E-MAIL : design@ppspl.in WEB SITE : www.ppspl.in Tel. : + 91 20 25232858				
PROJECT NUMBER		25-4035				
PROJECT NAME		ACXNMI-03				
		CLIENT				
		ADANICONNEX				
REINFORCEMENT DETAILS OF		N3C-2-C129				
PRECAST COLUMN :						
DWG NUMBER		N3C-2-C129-RF1				
REVISION CHECKED BY	APPROVAL		NAME	DATE	SCALE : AS SHOWN	
	TENDER		DRAWN	YRR		22-06-2026
	CONSTRUCTION	✓	CHECKED	SAM	22-06-2026	SIZE : A2
	INFORMATION		APPROVED	SDK	22-06-2026	
						REV. : R0