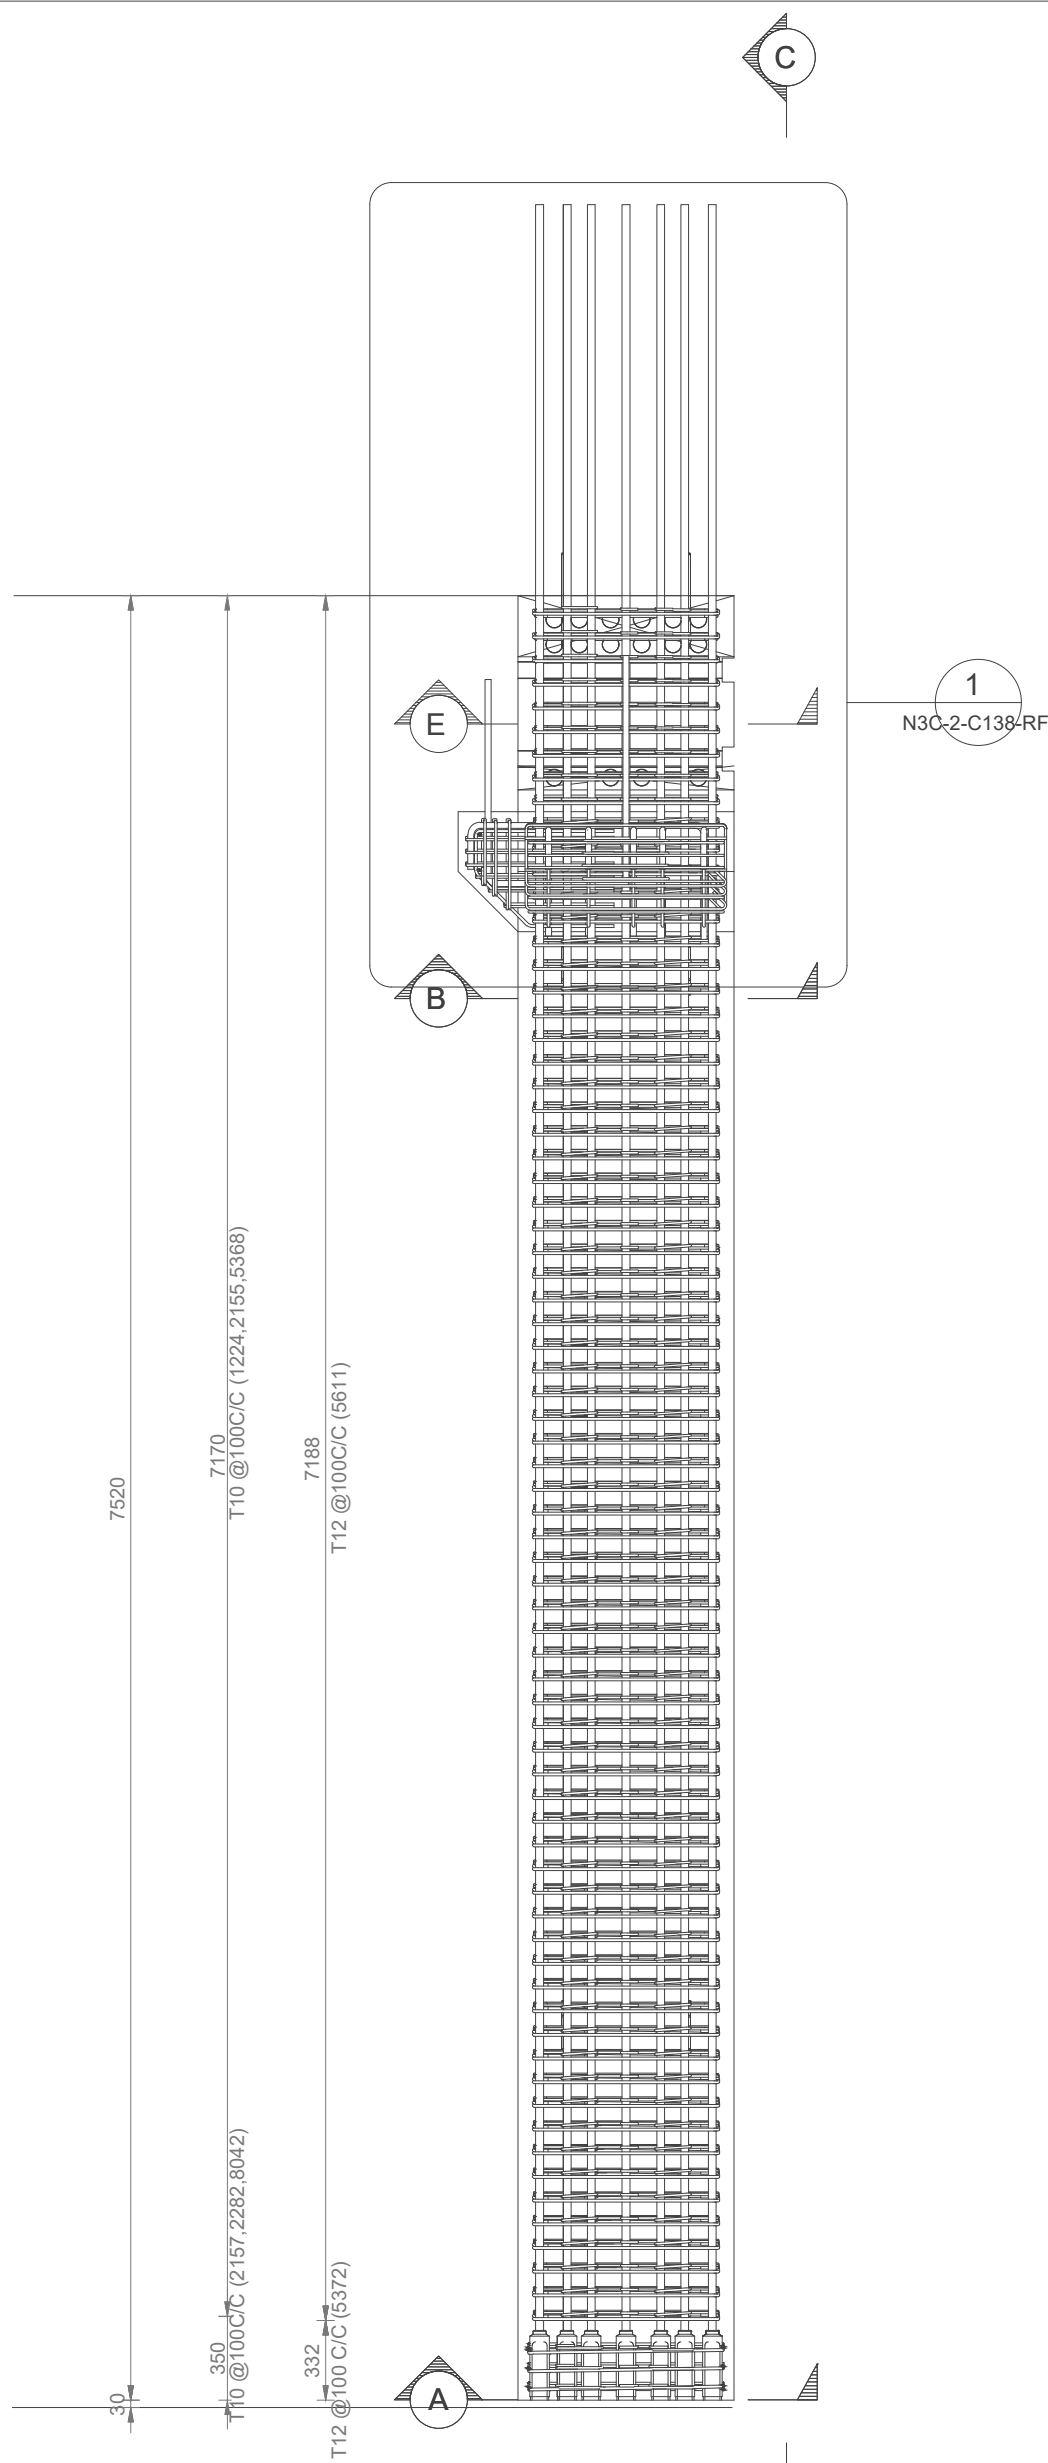
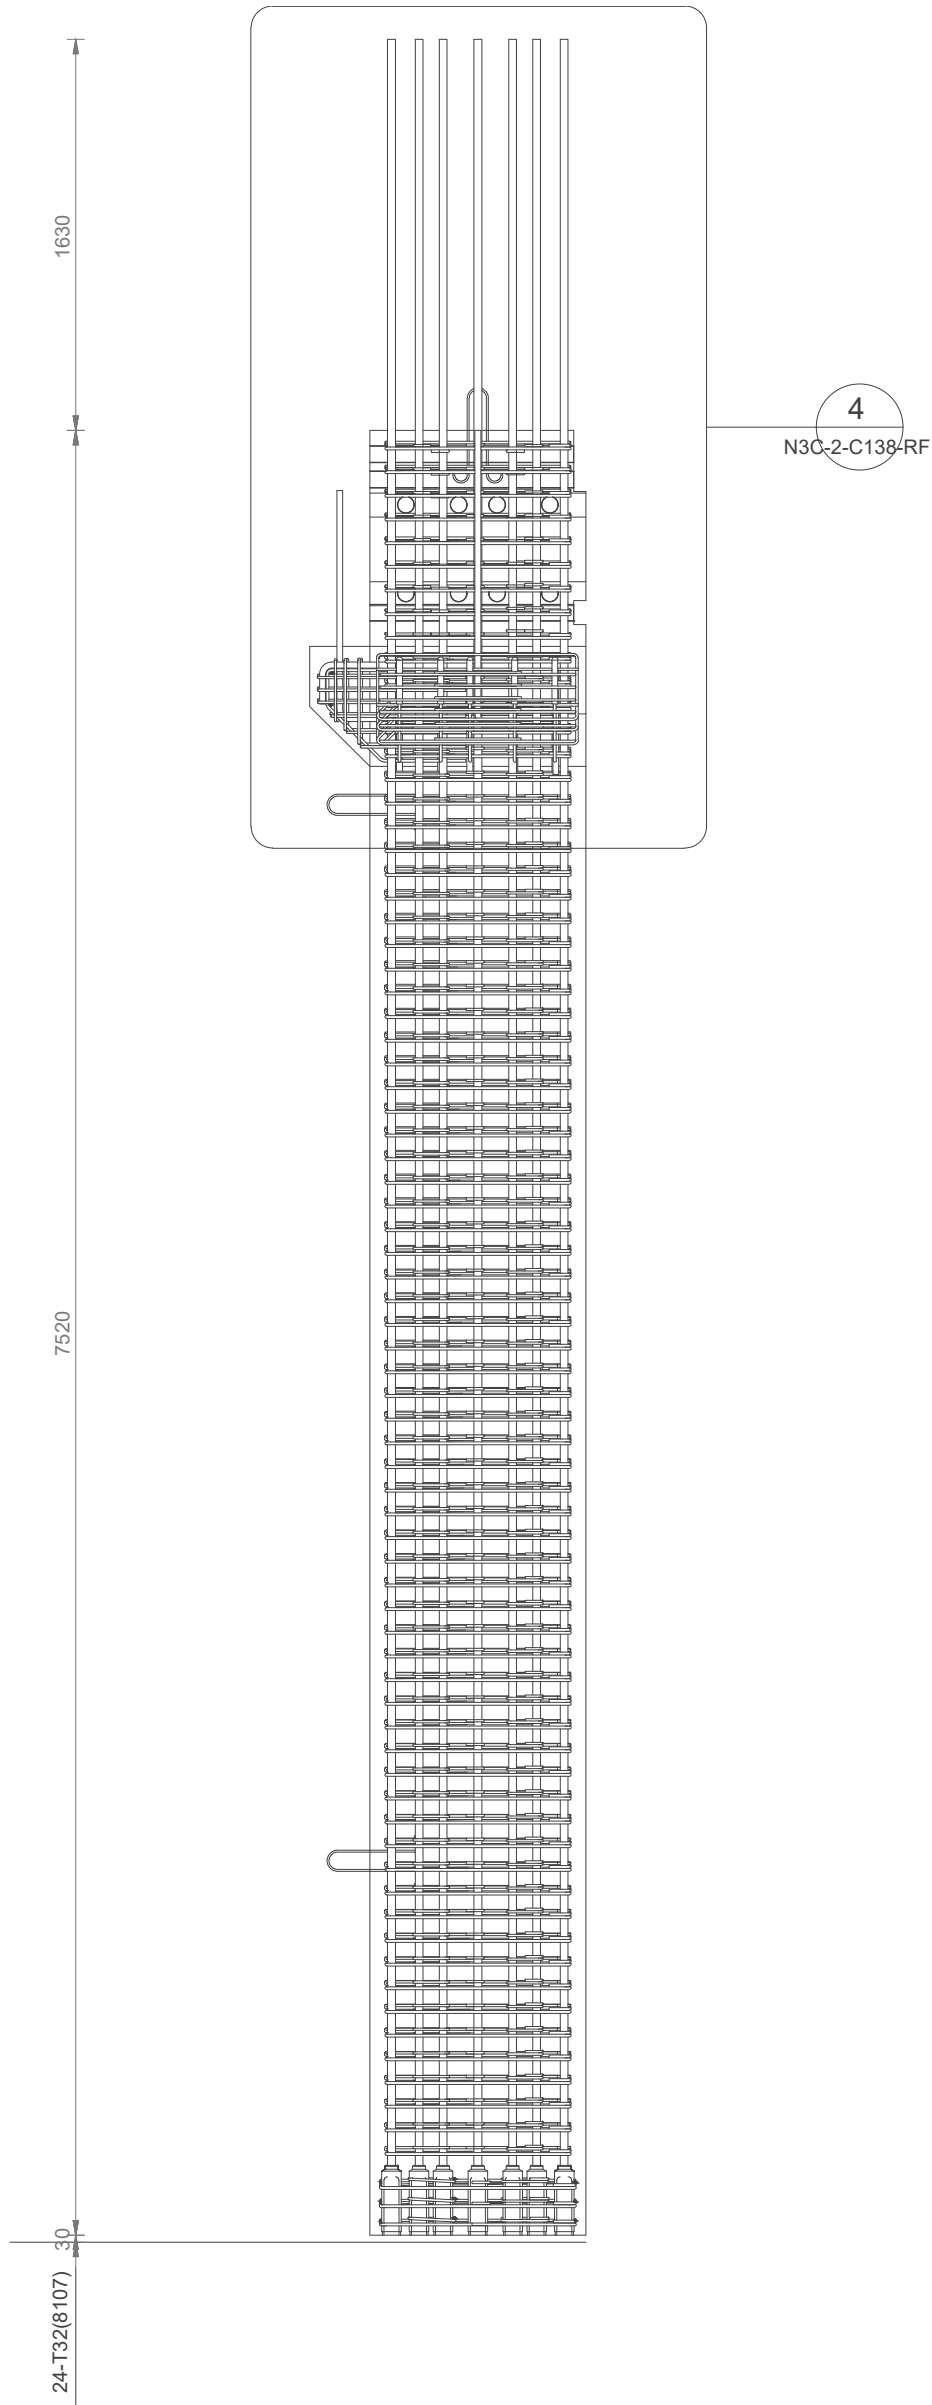
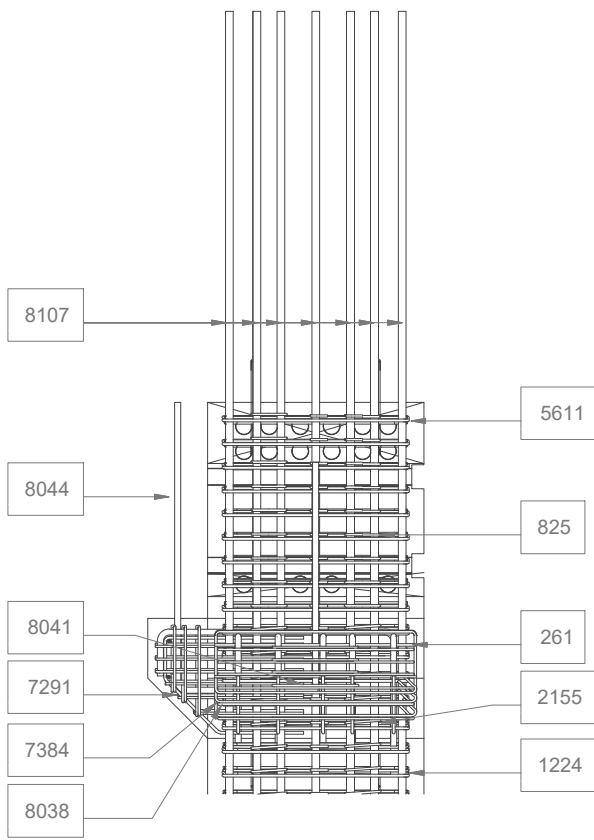
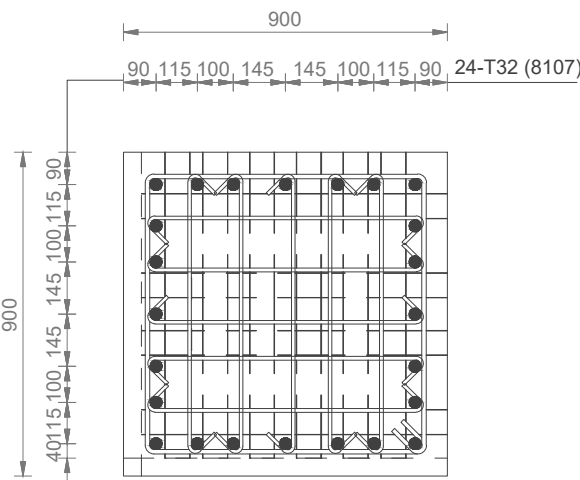
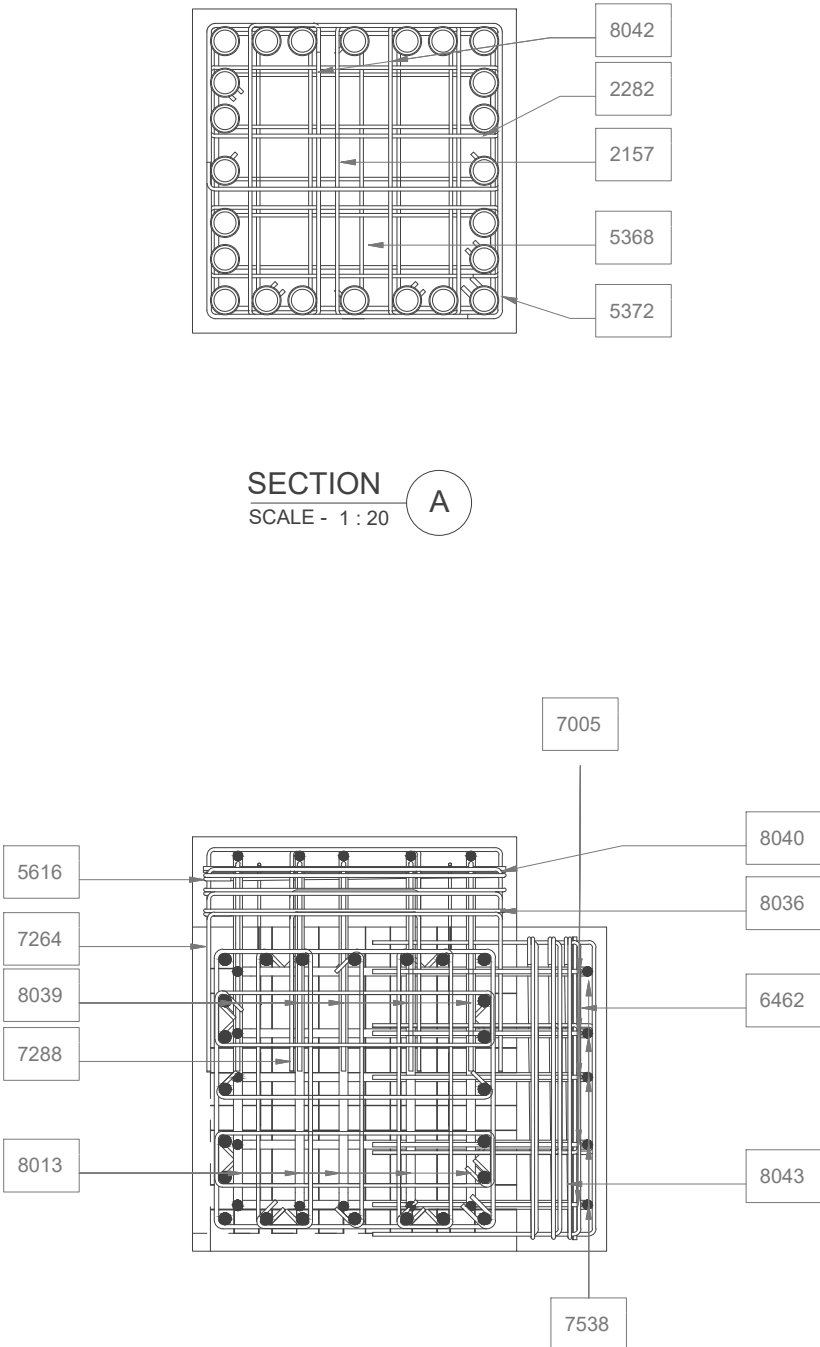





REINFORCEMENT DETAILS OF PRECAST COLUMN
SCALE = 1 : 30



ELEVATION
SCALE - 1 : 30




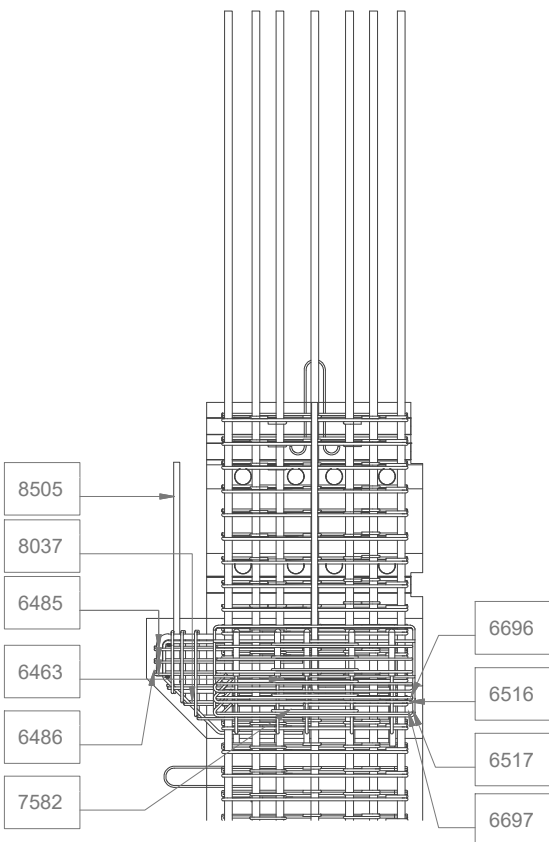DETAIL
SCALE - 1 : 30




DETAIL
SCALE - 1 : 30


R0	29-06-2026	GOOD FOR CONSTRUCTION	RAA	SAM	SDK
REV.	DATE	DRAWING STATUS	DRAWN BY	CHECKED BY	APPROVED BY
REVISION HISTORY					
STRUCTURAL CONSULTANT :		PPS ENGINEERING CONSULTANTS LLP.			
		FIRST FLOOR, SERVICE BUILDING, BAFI BHAVAN, DR. MANISHAI DESAI NAGAR, WARJE, PUNE 411058, INDIA. E-MAIL : design@ppspl.in WEB SITE : www.ppspl.in Tel. : + 91 20 25232858			
PROJECT NUMBER		25-4035			
PROJECT NAME		ACXNMI-03			
		CLIENT ADANICONNEX			
REINFORCEMENT DETAILS OF PRECAST COLUMN :		N3C-2-C138			
DWG NUMBER		N3C-2-C138-RF			
RELEASED FOR	APPROVAL		NAME	DATE	SCALE : AS SHOWN SIZE : A2 REV : R0
	TENDER		RAA	29-06-2026	
	CONSTRUCTION	✓	SAM	29-06-2026	
	INFORMATION		SDK	29-06-2026	

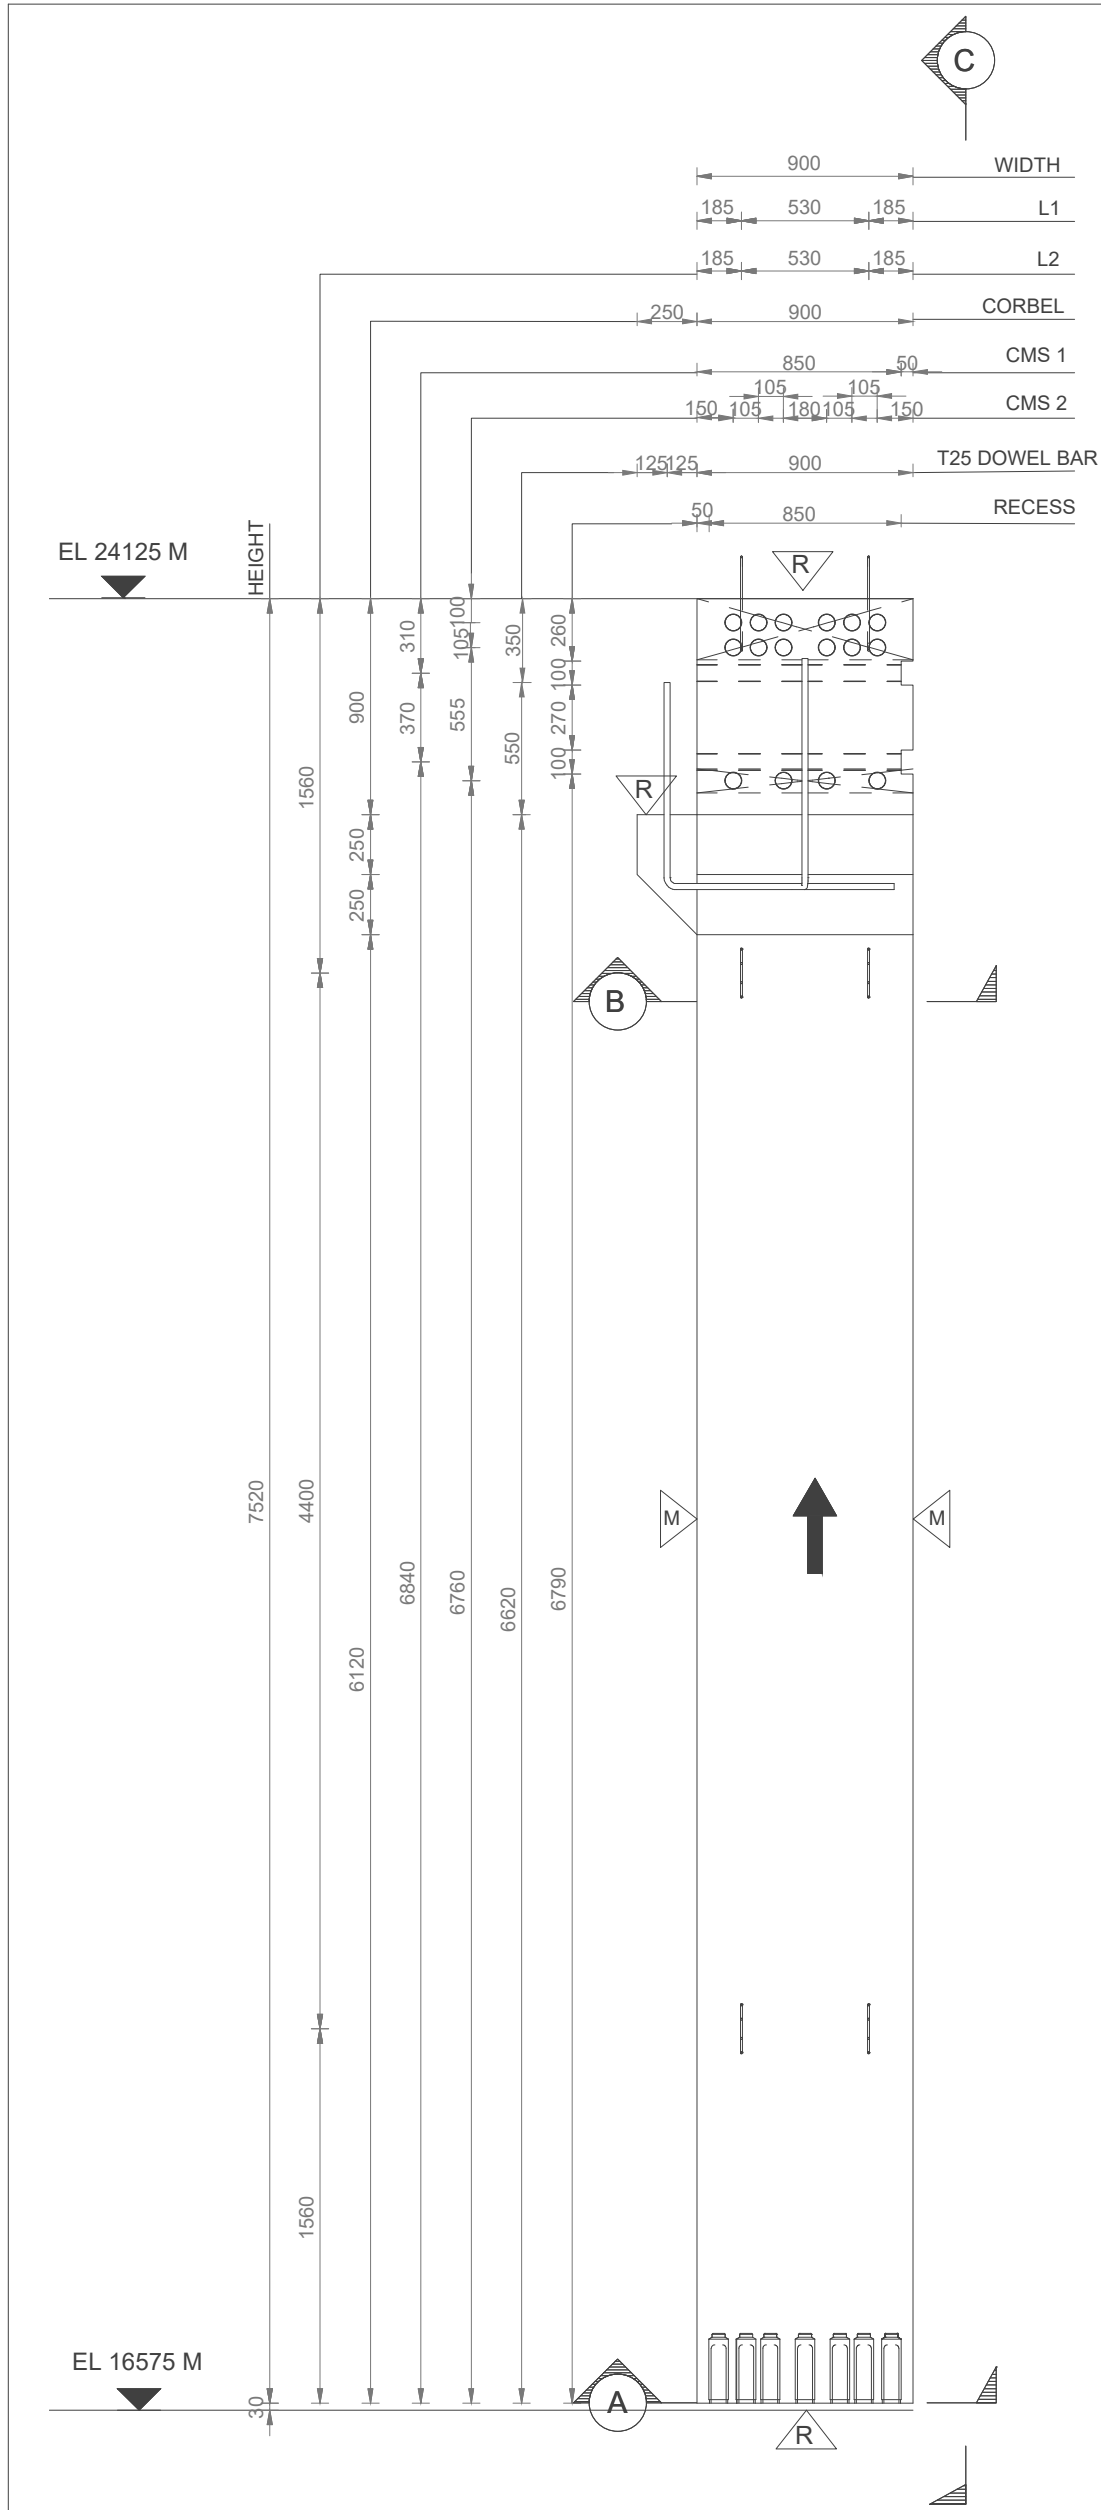

DETAIL OF PRECAST COLUMN
SCALE = 1 : 30

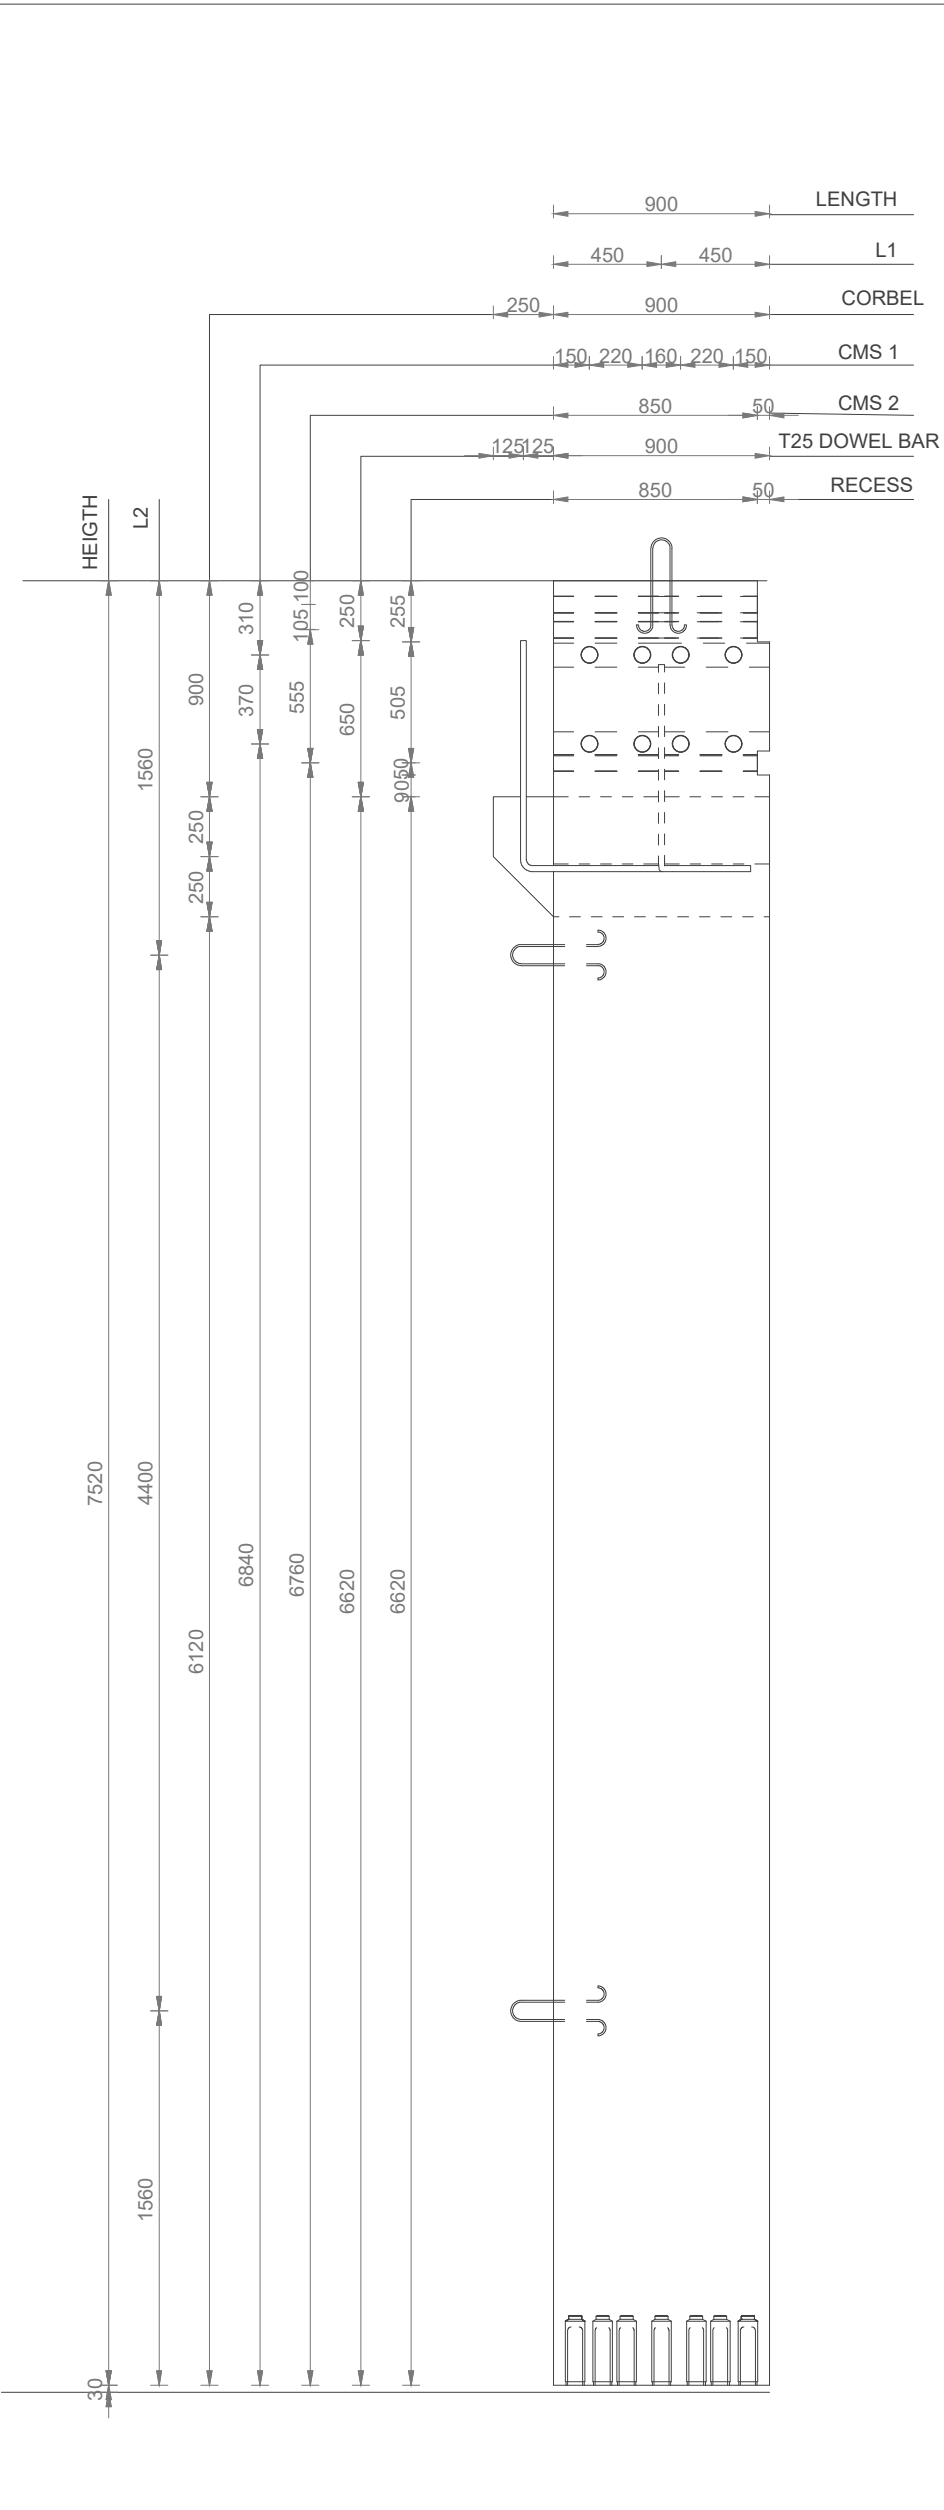


ELEVATION
SCALE - 1 : 30

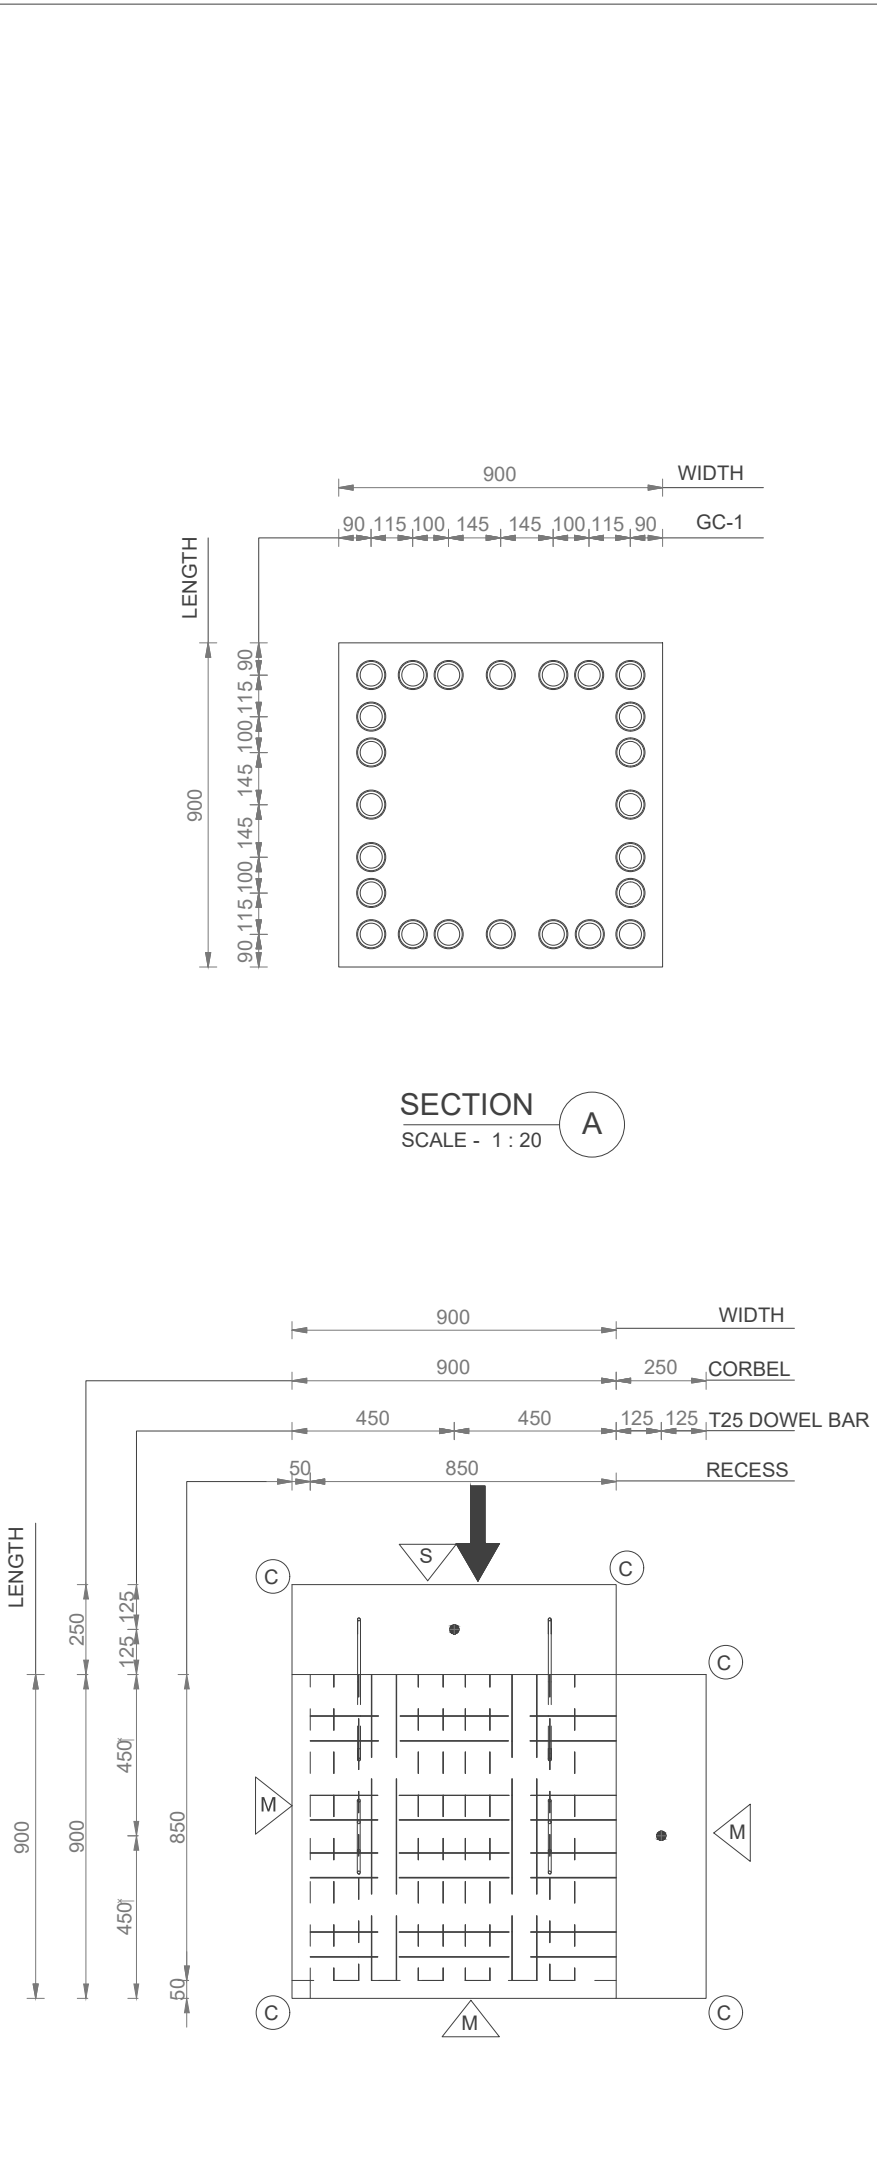


SECTION A
SCALE - 1 : 20

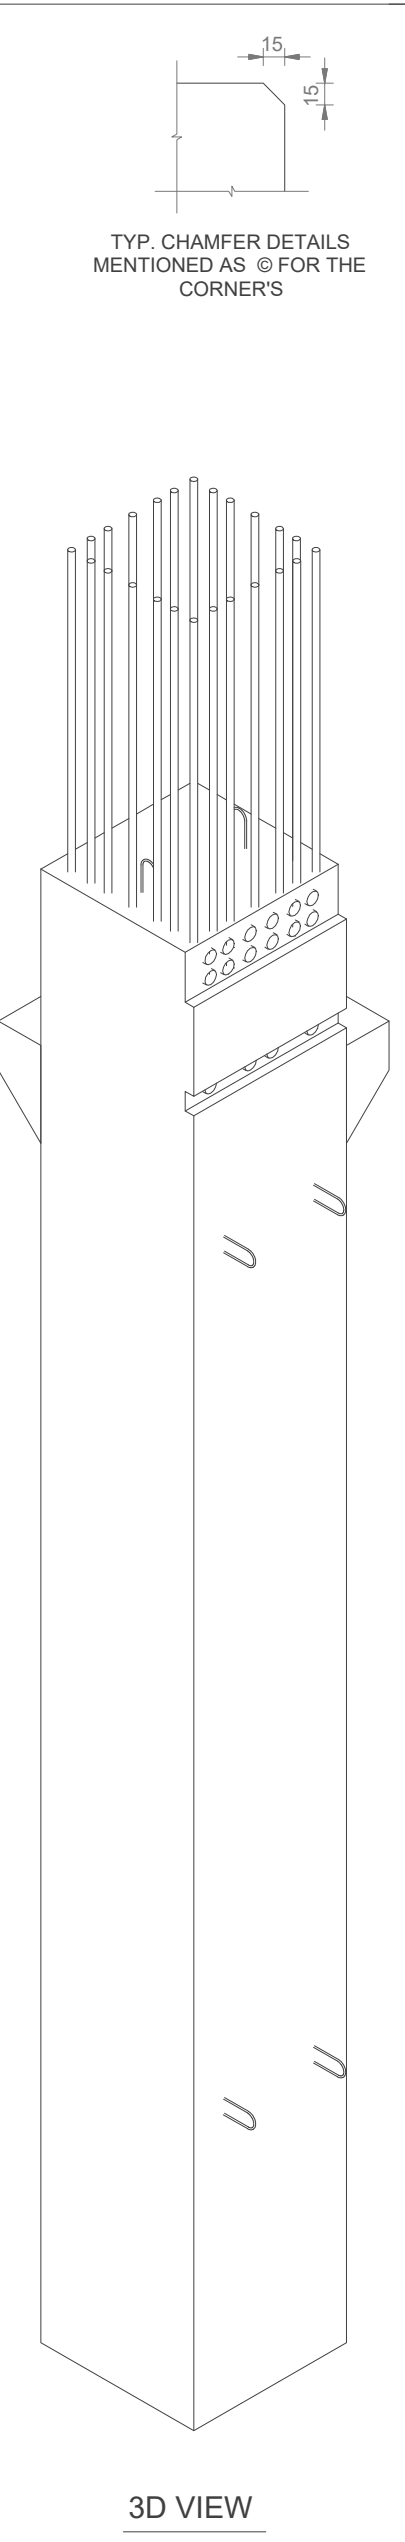SECTION B
SCALE - 1 : 20




3D VIEW

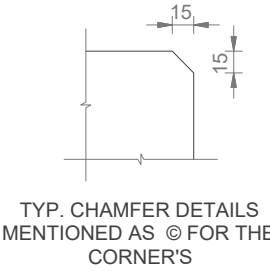

TYP. CHAMFER DETAILS
MENTIONED AS © FOR THE
CORNER'S


- LEGEND:-**
- RAKED SURFACE
 - SMOOTH FINISH
 - MOULD FINISH
 - CHAMFER 15x15
 - ERECTION MARK / VIEW DIRECTION

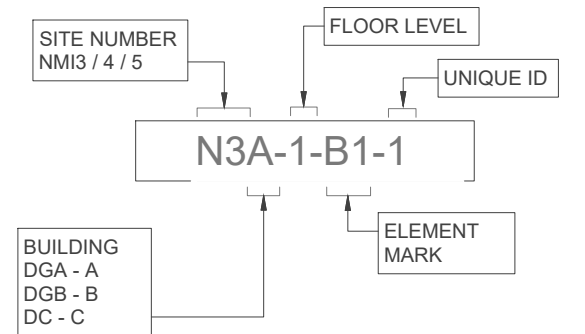- NOTES:**
- ALL DIMENSIONS ARE IN MM AND FOLLOW WRITTEN DIMENSIONS, DO NOT MEASURE.
 - CLEAR COVER FOR :
 - A. PRECAST COLUMN = 60mm
 - B. PRECAST COLUMN CORBEL = 30mm
 - GRADE OF REINFORCING STEEL, Fe 550D -TMT BARS CONFORMING TO IS1786:2008 WITH MINIMUM YIELD STRENGTH OF 550 N/mm²
 - CONCRETE STRENGTH :
 - A. AFTER 28 DAYS : @ M70
 - B. DEMOULDING & LIFTING : @ M20
 - C. TRANSPORTATION & ERECTION : @ M50
- DEMOLDING METHOD : HORIZONTAL
- STACKING METHOD : HORIZONTAL
- TRANSPORT METHOD : HORIZONTAL
- ERECTION METHOD : NO. OF LIFTER AS PER SHOP DRAWING




















MARK	DESCRIPTION	QTY.
CMS-1	70 DIA PIC SLEEVE	8
CMS-2	70 DIA PIC SLEEVE	16
GC-1	Ø32 GROUTC COUPLER 'L' TYPE	24
L1	LIFTER-15 TON CAPACITY EACH	2
L2	LIFTER-10 TON CAPACITY EACH	4
Grand total: 54		
















PRECAST COLUMN VOLUME (M³)	PRECAST COLUMN WEIGHT (TONNES)
6.17	16.34

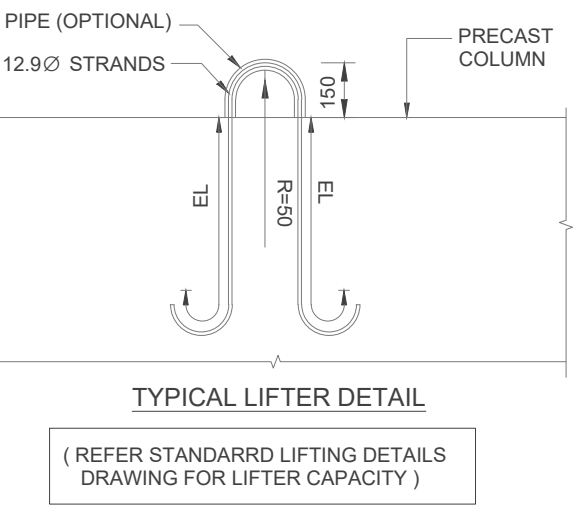

REFERENCE DRAWING					
DRAWING NO.			DESCRIPTION		
N3C-2-C138 -RF			REINFORCEMENT DETAILS OF PRECAST		
N3C-2-C138 -RF1			REINFORCEMENT DETAILS OF PRECAST		
			COLUMN -N3C-2-C138		
R0	29-06-2026	GOOD FOR CONSTRUCTION	RAA	SAM	SDK
REV.	DATE	DRAWING STATUS	DRAWN BY	CHECKED BY	APPROVED BY
REVISION HISTORY					
STRUCTURAL CONSULTANT:		PPS ENGINEERING CONSULTANTS LLP			
		FIRST FLOOR, SERVICE BUILDING, BAFI BHAVAN, DR. MANISHAI DESAI NAGAR, WARJE, PUNE 411058, INDIA. EMAIL : design@ppsppl.in			
		WEB SITE : www.ppspl.in Tel. : + 91 20 25232858			
PROJECT NUMBER			25-4035		
PROJECT NAME			ACXNMI-03		
 Your Growth. Our Priority.			CLIENT		
			ADANICONNEX		
DETAILS OF PRECAST COLUMN : N3C-2-C138					
DWG NUMBER			N3C-2-C138-F		
RELEA SED FOR	APPROVAL		NAME	DATE	SCALE : AS SHOWN SIZE : A2 REV. : R0
	TENDER		DRAWN	29-06-2026	
	CONSTRUCTION	✓	CHECKED	SAM 29-06-2026	
	INFORMATION		APPROVED	SDK 29-06-2026	

ELEMENT NO.	REQUIRED NO.
N3C-2-C138	01
TOTAL	01

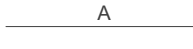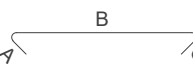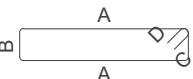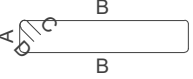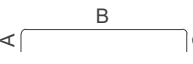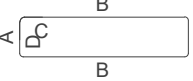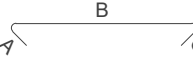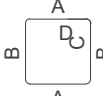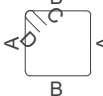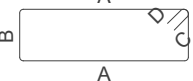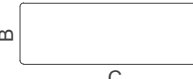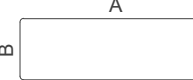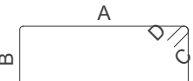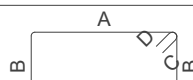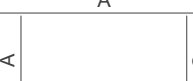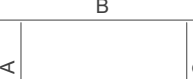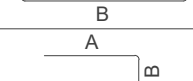N3C-2-C138 REBAR SCHEDULE										
BENDING DIMENSIONS										
BAR MARK	BAR DIAMETER	QTY.	BENDING DETAILS	A	B	C	D	BAR CUTTING LENGTH	TOTAL BAR LENGTH	TOTAL WEIGHT
261	10	4		840	0	0	0	840	3400	2.10 kg
825	10	45		80	775	80	0	935	42750	26.39 kg
1224	10	64		775	155	80	80	1971	126400	78.03 kg
2155	10	192		155	775	80	80	1971	379200	234.09 kg
2157	10	6		80	820	80	0	947	5700	3.52 kg
2282	10	3		200	818	80	80	2114	6375	3.94 kg
5368	10	173		80	765	80	0	925	160025	98.79 kg
5372	12	3		820	820	96	96	3373	10125	9.00 kg
5611	12	73		776	780	96	96	3245	237250	210.90 kg
5616	10	1		840	264	80	80	2318	2325	1.44 kg
6462	10	1		578	820	578	300	1943	1950	1.20 kg
6463	10	1		578	363	578	300	1487	1500	0.93 kg
6485	10	6		620	820	620	300	2027	12300	7.59 kg
6486	10	6		620	363	620	300	1570	9450	5.83 kg
6516	10	1		840	323	80	80	2437	2450	1.51 kg
6517	10	1		840	380	80	80	2551	2575	1.59 kg
6696	10	1		525	820	525	300	1838	1850	1.14 kg
6697	10	1		460	820	460	300	1707	1725	1.06 kg
7005	12	5		582	183	319	0	1409	7125	6.33 kg

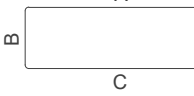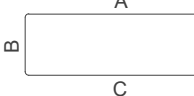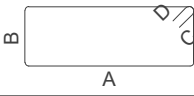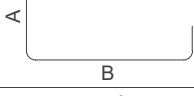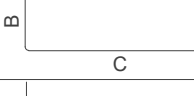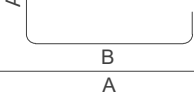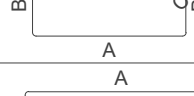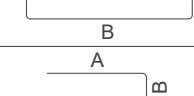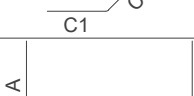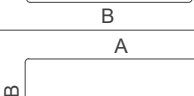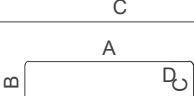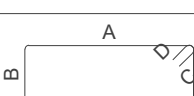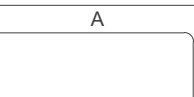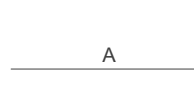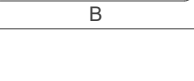N3C-2-C138 REBAR SCHEDULE										
BENDING DIMENSIONS										
BAR MARK	BAR DIAMETER	QTY.	BENDING DETAILS	A	B	C	D	BAR CUTTING LENGTH	TOTAL BAR LENGTH	TOTAL WEIGHT
7264	10	1		441	820	441	300	1669	1675	1.03 kg
7288	10	1		442	363	442	300	1214	1225	0.76 kg
7291	10	1		526	363	526	300	1383	1400	0.86 kg
7384	10	1		840	302	80	80	2395	2400	1.48 kg
7538	25	5		488	997	195	300	1597	8000	30.87 kg
7582	10	1		461	363	461	300	1251	1275	0.79 kg
8013	25	5		467	997	175	300	1557	7875	30.38 kg
8036	10	1		840	361	80	80	2513	2525	1.56 kg
8037	10	1		495	363	495	300	1320	1325	0.82 kg
8038	10	1		500	820	500	300	1787	1800	1.11 kg
8039	12	5		582	158	328	0	1387	7000	6.22 kg
8040	10	1		565	820	565	300	1917	1925	1.19 kg
8041	10	1		568	363	568	300	1466	1475	0.91 kg
8042	10	9		818	200	80	80	2114	19125	11.81 kg
8043	10	1		840	280	80	80	2351	2375	1.47 kg
8044	25	1		863	963	0	0	2134	2150	6.94 kg
8107	32	24		8895	0	0	0	8895	213600	1375.68 kg
8505	25	1		963	963	0	0	1884	1900	7.33 kg
		648							1293525	2154.67 kg

N3C-2-C138 REBAR SCHEDULE SUMMARY		
BAR DIAMETER	TOTAL BAR LENGTH	TOTAL WEIGHT
10	798500	495.07 kg
12	261500	232.74 kg
25	19925	76.91 kg
32	213600	1349.95 kg
1293525		2154.67 kg

R0	29-06-2026	GOOD FOR CONSTRUCTION	RAA	SAM	SDK
REV.	DATE	DRAWING STATUS	DRAWN BY	CHECKED BY	APPROVED BY
REVISION HISTORY					
STRUCTURAL CONSULTANT :		PPS ENGINEERING CONSULTANTS LLP.			
		FIRST FLOOR, SERVICE BUILDING, BAFI BHAVAN, DR. MANIBHAI DESAI NAGAR, WARJE, PUNE 411058, INDIA. EMAIL : design@ppsel.in WEB SITE : www.ppsel.in Tel. : + 91 20 25232858			
		PROJECT NUMBER		25-4035	
		PROJECT NAME		ACXNMI-03	
				CLIENT	
		ADANICONNEX			
REINFORCEMENT DETAILS OF N3C-2-C138 PRECAST COLUMN :					
DWG NUMBER		N3C-2-C138-RF1			
CHECKED BY	APPROVAL		NAME	DATE	SCALE : AS SHOWN SIZE : A2 REV. : R0
	TENDER		DRAWN	RAA	
	CONSTRUCTION	✓	CHECKED	SAM	
	INFORMATION		APPROVED	SDK	
				29-06-2026	